


План 1-го этажа. Система отопления
М 1:100

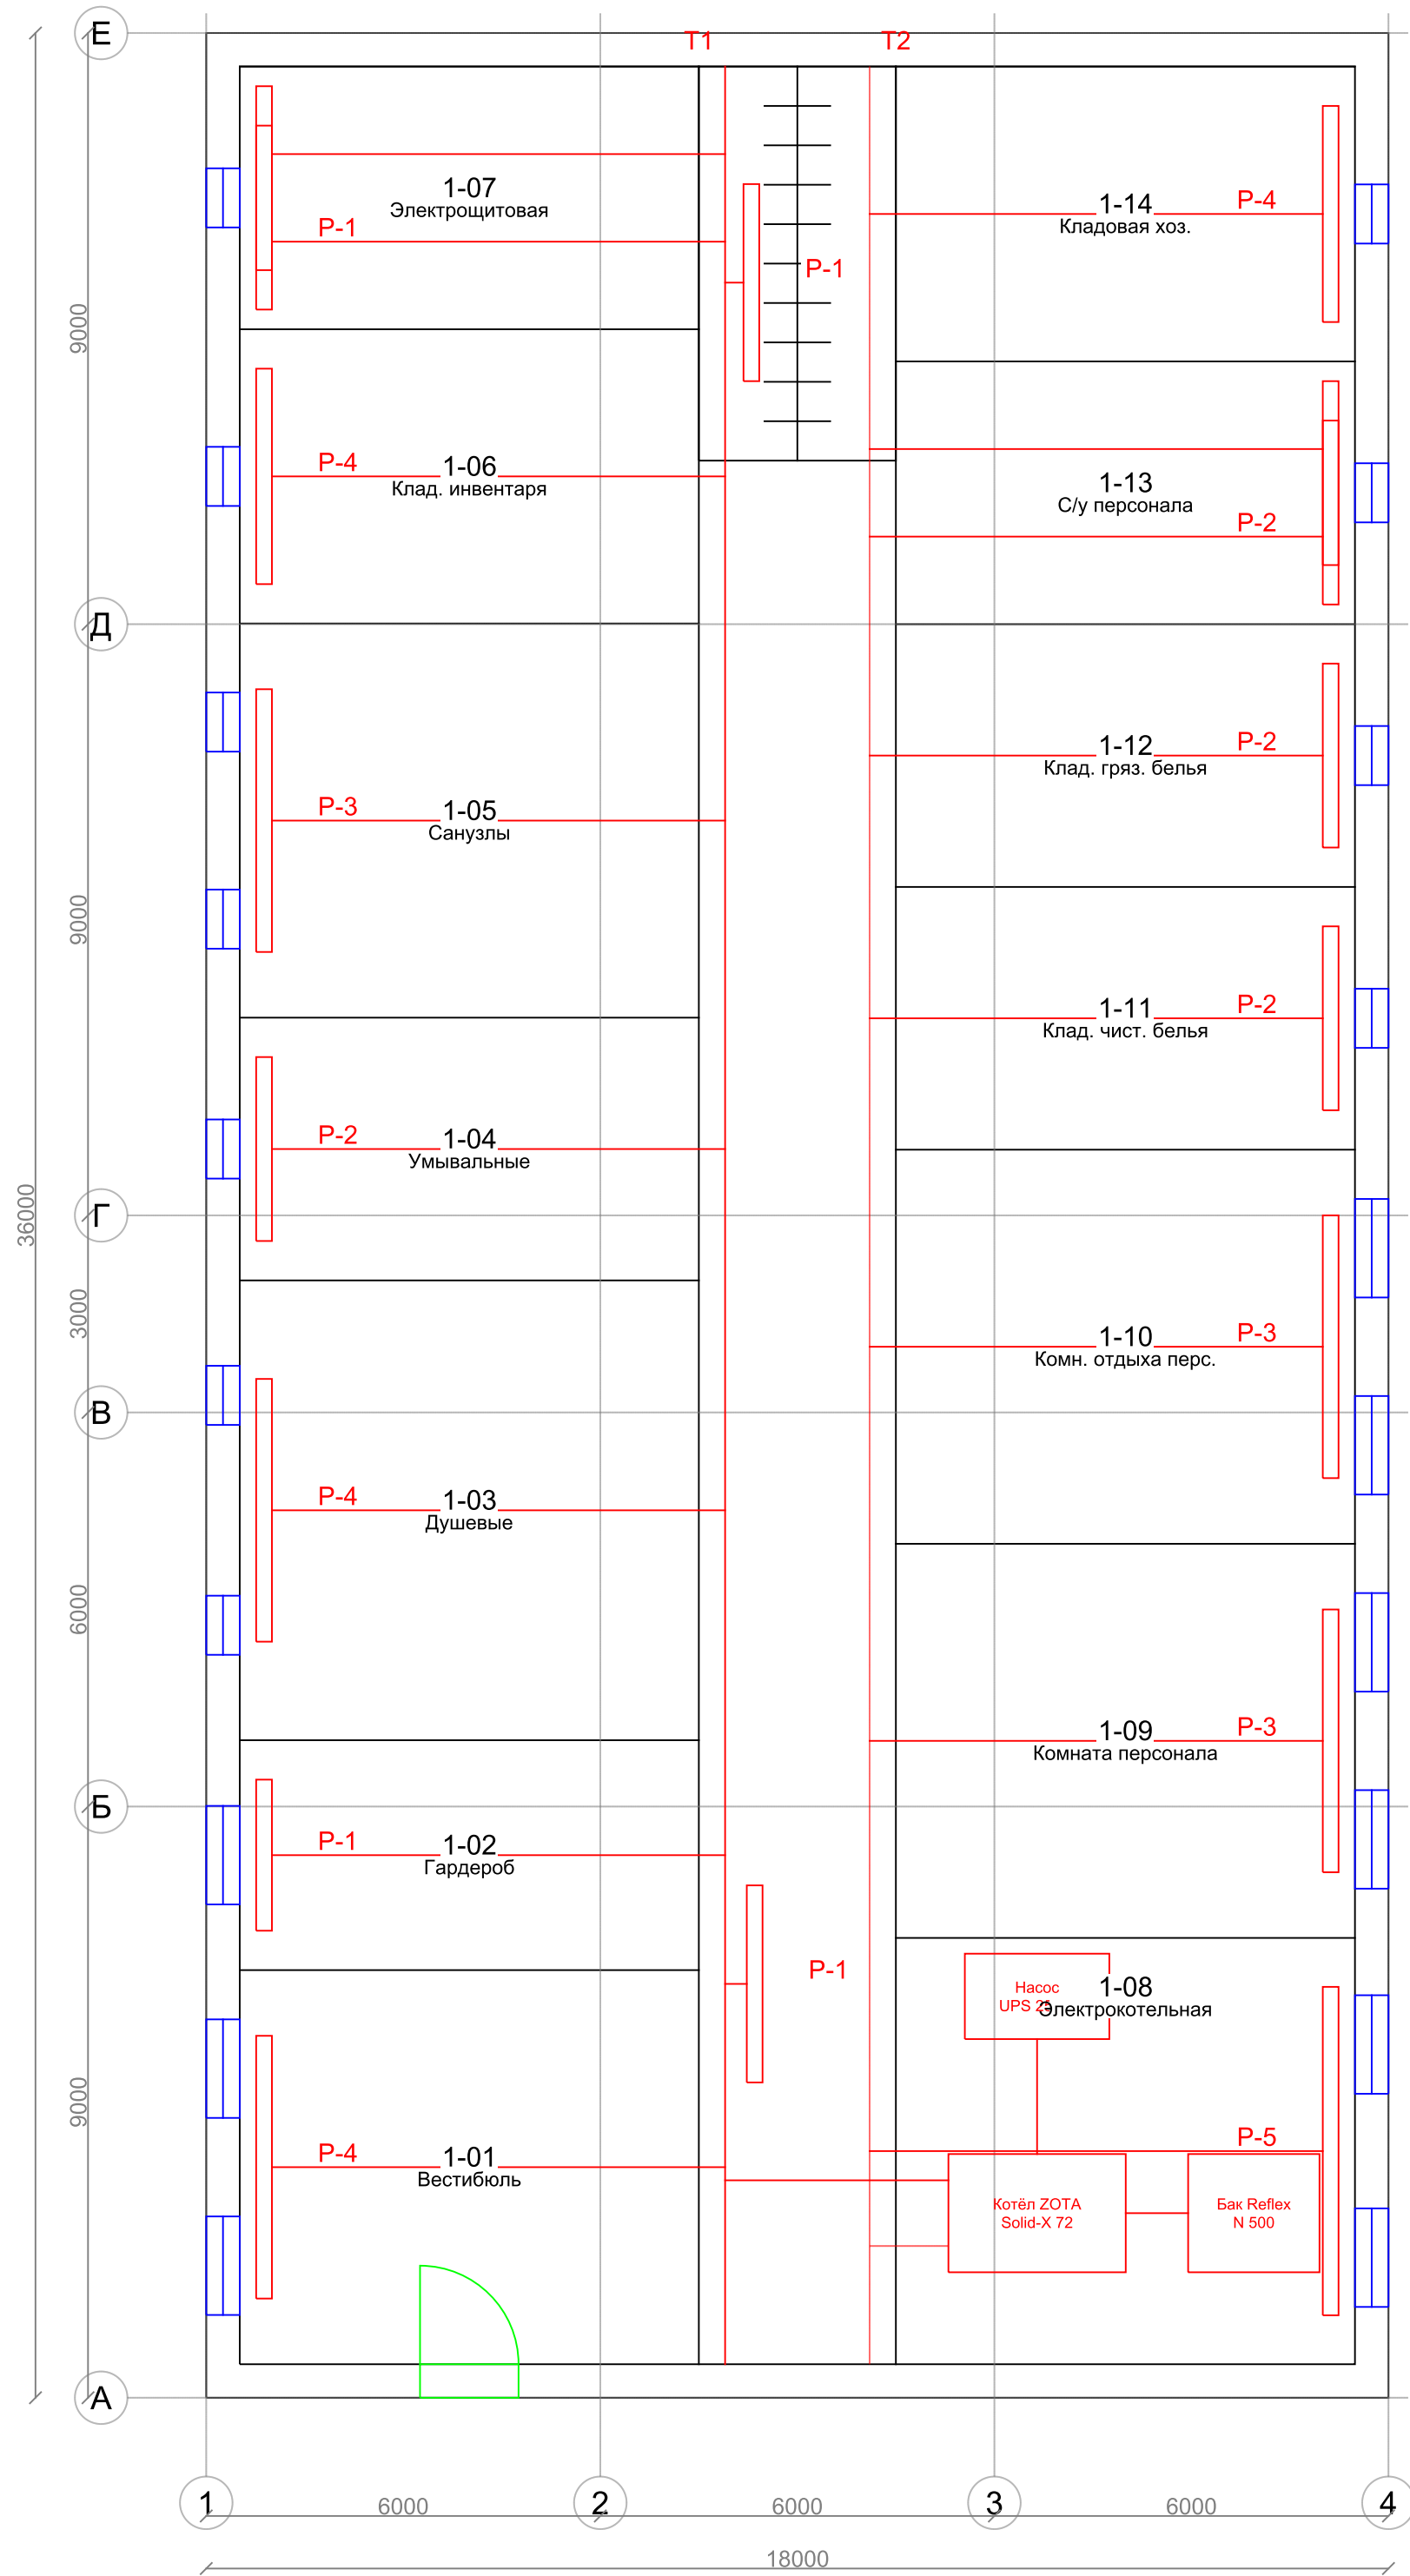

Примечания

- Система отопления двухтрубная с верхней разводкой.
- Теплоноситель — вода 95–70 °С; t_{ср} = 82,5 °С.
- Отопительные приборы — регистры из стальных труб $\varnothing 108 \times 4$ (ГОСТ 10704); окраска масляной краской в 2 слоя.
- Источник теплоты — электроды ZOTA Solid-X 72 (72 кВт), помещение электростанции 1-08.
- Размеры на чертеже — в мм, отметки — в м.

Экспликация помещений

№	Наименование	Размеры, м	S, м²
1-01	Вестибюль (главный вход)	6×6,99	41,9
1-02	Гардероб	3,5×6,99	24,5
1-03	Душевые	7×6,99	48,9
1-04	Умывальные	4×6,99	28
1-05	Санузлы (общие)	6×6,99	41,9
1-06	Кладовая инвентаря	4,48×6,99	31,3
1-07	Электрощитовая	4×6,99	28
1-08	Электростанция	6,49×6,99	45,4
1-09	Комната персонала	6×6,99	41,9
1-10	Комната отдыха персонала	6×6,99	41,9
1-11	Кладовая чистого белья	4×6,99	28
1-12	Кладовая грязного белья	4×6,99	28
1-13	Санузел персонала	4×6,99	28
1-14	Кладовая хозяйственная	4,49×6,99	31,4
1-15	Коридор, лестничная клетка	34,98×3	104,9

Условные обозначения

	Регистр из стальных труб $\varnothing 108 \times 4$, Р-1...Р-5
	T1 — магистраль подающая
	T2 — магистраль обратная
	Стояк, подводка к прибору
	Электроды ZOTA Solid-X 72
	Насос Grundfos UPS 25-60
	Бак расширительный Reflex N 500

Бытовой корпус базы отдыха «Дубрава» Система отопления. План 1-го этажа						МИВУ.080301.018-ОВ		
						Стадия	Лист	Листов
Изм.	Лист	№ докум.	Подп.	Дата	М 1:100	ВКР	1	6
Разраб.	Лукашин А. О.	Полуляк Г.Л.				Муромский институт (филиал) ВлГУ кафедра ТБ		
Руковод.	—							
Н. контр.	Шарапов Р.В.							
Утв.					Стадия — ВКР			
					2026 г.			