


План 2-го этажа. Система отопления
М 1:100

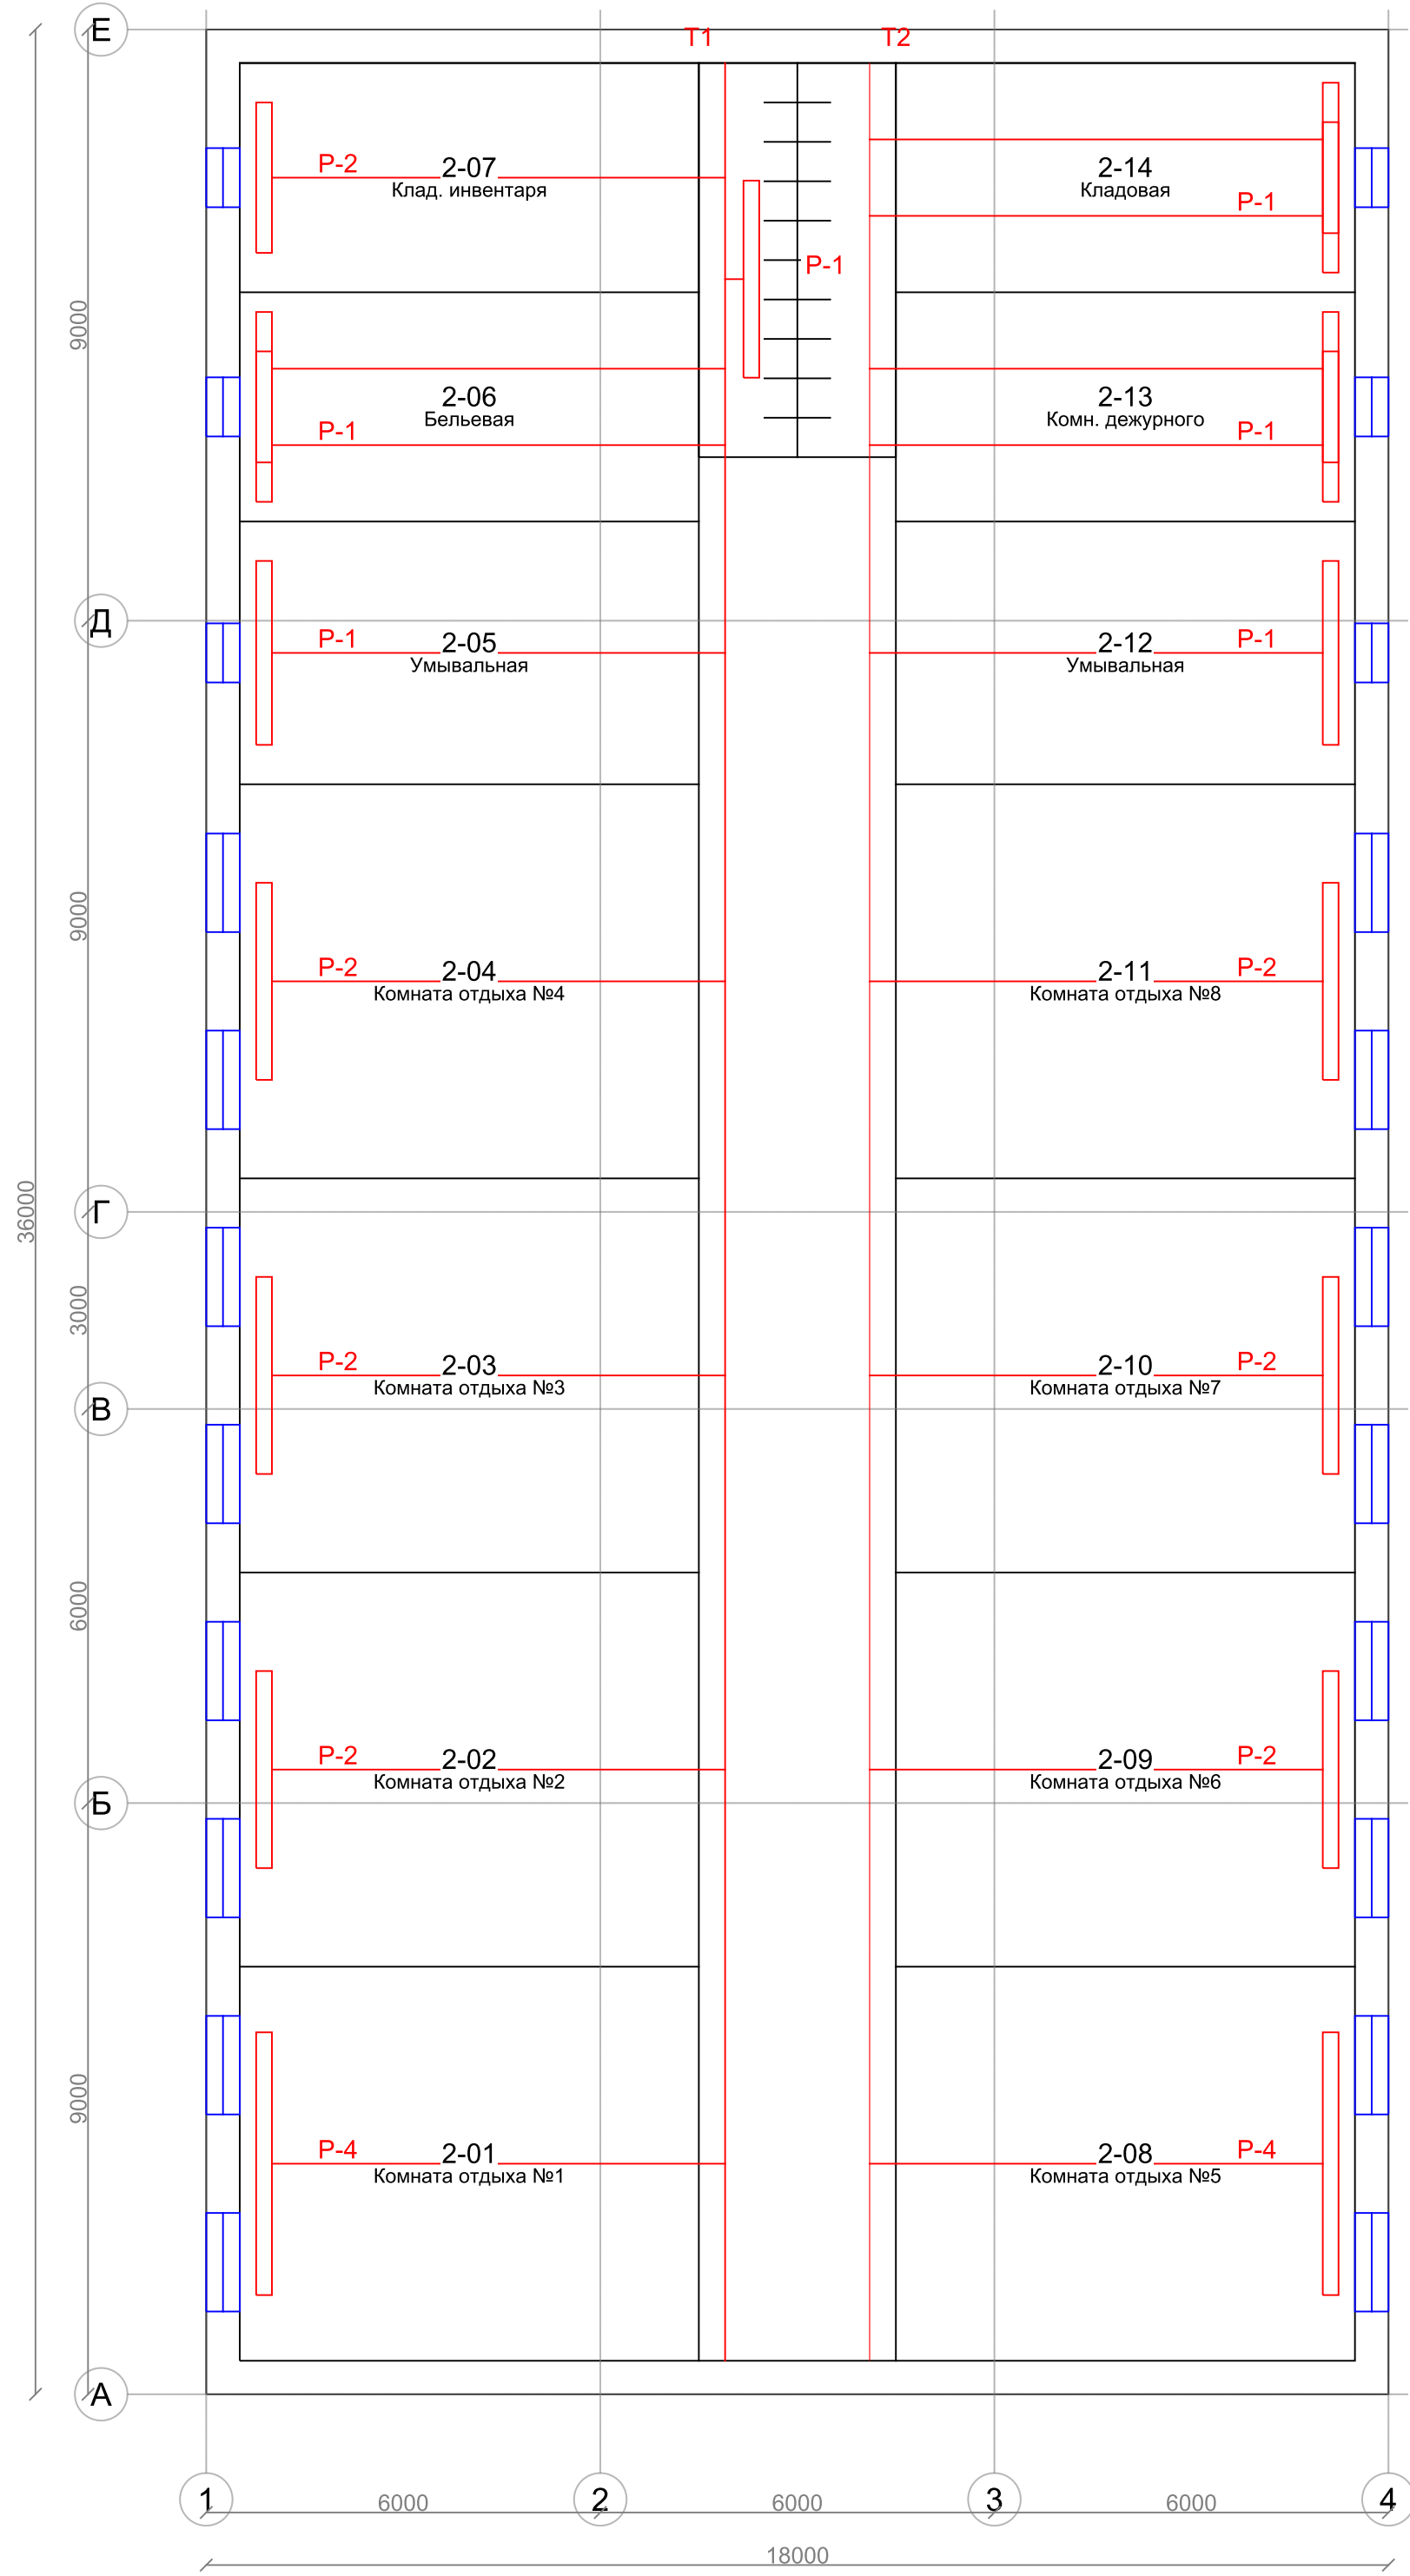

Примечания

- Система отопления двухтрубная с верхней разводкой.
- Теплоноситель — вода 95–70 °С; t_{ср} = 82,5 °С.
- Отопительные приборы — регистры из стальных труб $\varnothing 108\times 4$ (ГОСТ 10704); окраска масляной краской в 2 слоя.
- Источник теплоты — электродотепл ZOTA Solid-X 72 (72 кВт), помещение электродотепльной 1-08 (лист 1).
- Размеры на чертеже — в мм, отметки — в м.

Экспликация помещений

№	Наименование	Размеры, м	S, м²
2-01	Комната отдыха №1	6×6,99	41,9
2-02	Комната отдыха №2	6×6,99	41,9
2-03	Комната отдыха №3	6×6,99	41,9
2-04	Комната отдыха №4	6×6,99	41,9
2-05	Умывальная (левая)	4×6,99	28
2-06	Бельевая	3,49×6,99	24,4
2-07	Кладовая инвентаря	3,49×6,99	24,4
2-08	Комната отдыха №5	6×6,99	41,9
2-09	Комната отдыха №6	6×6,99	41,9
2-10	Комната отдыха №7	6×6,99	41,9
2-11	Комната отдыха №8	6×6,99	41,9
2-12	Умывальная (правая)	4×6,99	28
2-13	Комната дежурного персонала	3,49×6,99	24,4
2-14	Кладовая	3,49×6,99	24,4
2-15	Коридор, лестничная клетка	34,98×3	104,9

Условные обозначения

	Регистр из стальных труб $\varnothing 108\times 4$, Р-1...Р-5
	T1 — магистраль подающая
	T2 — магистраль обратная
	Стояк, подводка к прибору
	Электродотепл ZOTA Solid-X 72
	Насос Grundfos UPS 25-60
	Бак расширительный Reflex N 500

Бытовой корпус базы отдыха «Дубрава» Система отопления. План 2-го этажа					МИВУ.080301.018-ОВ			
					Стадия		Лист	Листов
					ВКР		2	6
Изм.	Лист	№ докум.	Подп.	Дата	М 1:100			
Разраб.		Лукашин А. О.						
Руковод.		Полуляк Г.П.						
Н. контр.		—			Муромский институт (филиал) ВлГУ кафедра ТБ			
Утв.		Шарапов Р.В.						
					Стадия — ВКР			
					2026 г.			