


План 1-го этажа. Система вентиляции
М 1:100

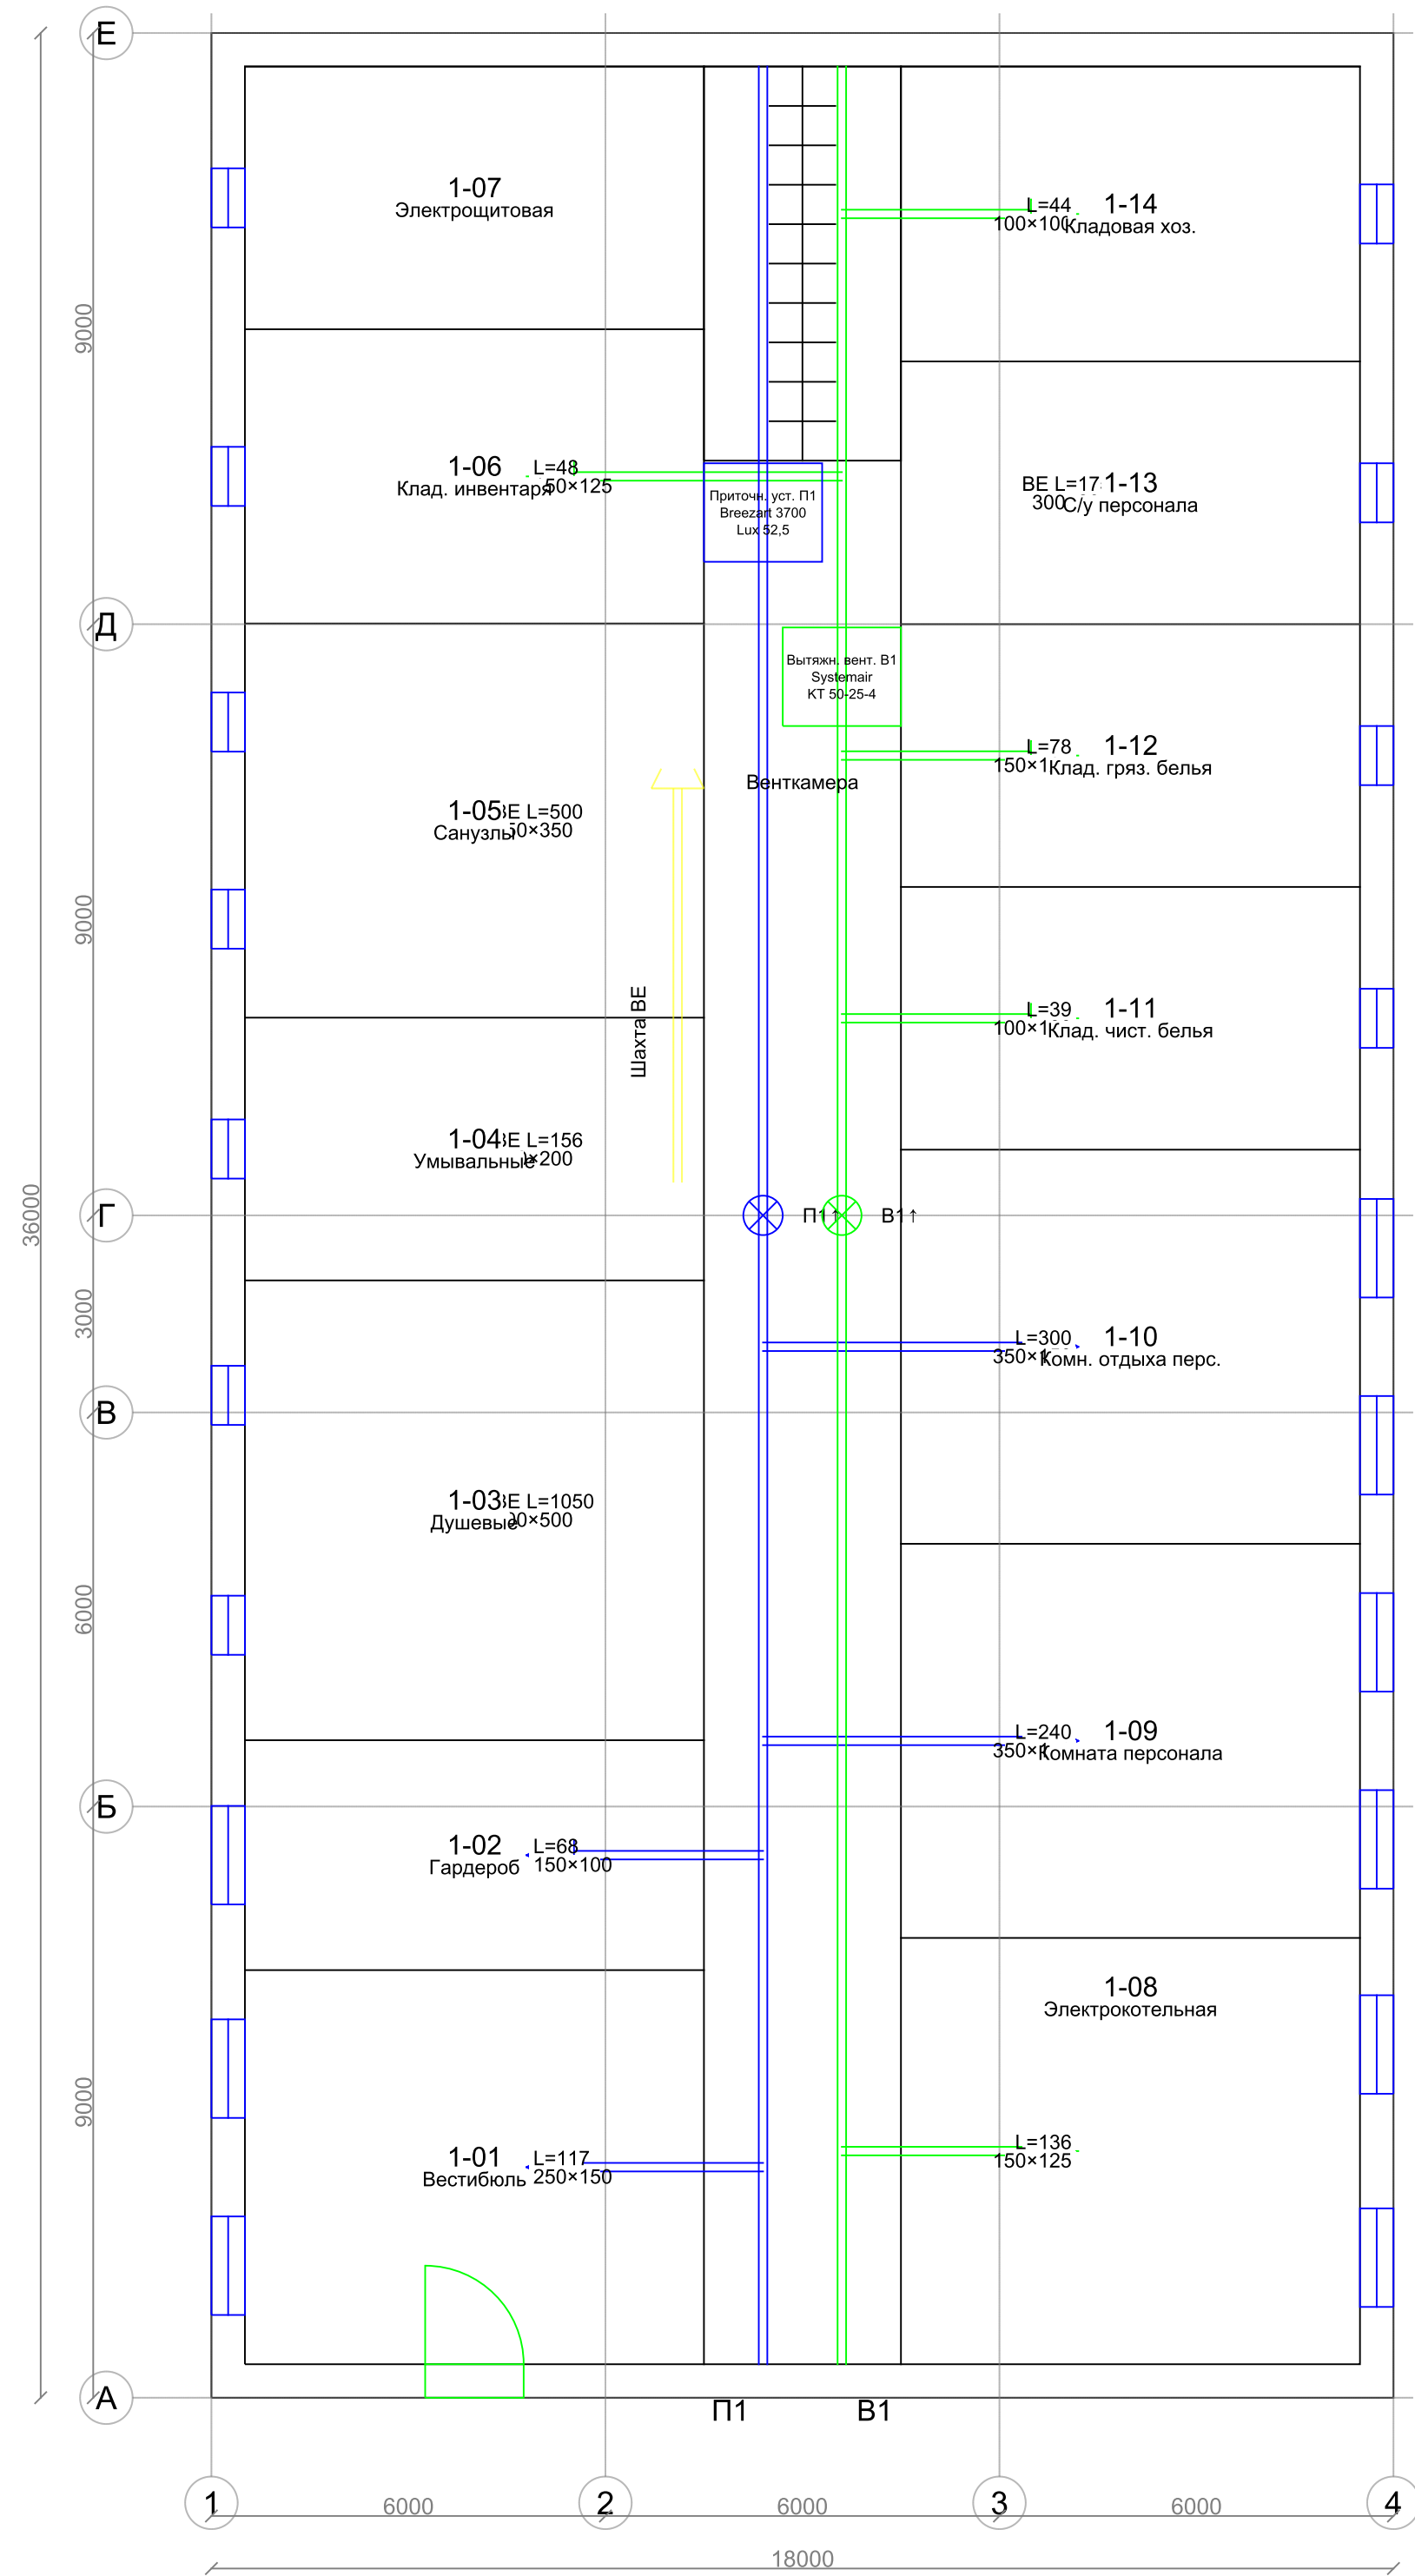

Примечания

- Вентиляция приточно-вытяжная с механическим и естественным побуждением (СП 60.13330.2020, СП 44.13330.2011).
- П1 — приток 3040 м³/ч, t_{прит} = +18 °С, Breezart 3700 Lux 52,5 (калорифер 52,5 кВт).
- В1 — мех. вытяжка 1180 м³/ч, Systemair KT 50-25-4.
- БЕ — естеств. вытяжка 2190 м³/ч из влажных помещений санблока (1 эт., лист 3).
- Воздуховоды стальные; сечения а×в даны у решёток.
- Размеры на чертеже — в мм, расходы L — в м³/ч.

Экспликация помещений

№	Наименование	Размеры, м	S, м²
1-01	Вестибюль (главный вход)	6×6,99	41,9
1-02	Гардероб	3,5×6,99	24,5
1-03	Душевые	7×6,99	48,9
1-04	Умывальные	4×6,99	28
1-05	Санузлы (общие)	6×6,99	41,9
1-06	Кладовая инвентаря	4,48×6,99	31,3
1-07	Электрощитовая	4×6,99	28
1-08	Электростанция	6,49×6,99	45,4
1-09	Комната персонала	6×6,99	41,9
1-10	Комната отдыха персонала	6×6,99	41,9
1-11	Кладовая чистого белья	4×6,99	28
1-12	Кладовая грязного белья	4×6,99	28
1-13	Санузел персонала	4×6,99	28
1-14	Кладовая хозяйственная	4,49×6,99	31,4
1-15	Коридор, лестничная клетка	34,98×3	104,9

Условные обозначения

	П1 — воздуховод приточный (синий)
	В1 — воздуховод вытяжной мех. (зелёный)
	БЕ — канал естеств. вытяжки (жёлт., штрих.)
	Решётка приточная (стрелка в помещ.)
	Решётка вытяжная (стрелка к каналу)
	Приточная установка Breezart 3700 Lux
	Вытяжной вентилятор Systemair KT 50-25-4
	Стояк (транзит П1/В1 между этажами)

Бытовой корпус базы отдыха «Дубрава» Система вентиляции. План 1-го этажа						МИВУ.080301.018-ОВ		
						Стадия	Лист	Листов
						ВКР	3	6
Изм.	Лист	№ докум.	Подп.	Дата	М 1:100	Муромский институт (филиал) ВлГУ кафедра ТБ		
Разраб.		Лукашин А. О.						
Руковод.		Полуляк Г.П.						
Н. контр.		—			Стадия — ВКР			
Утв.		Шарапов Р.В.						
					2026 г.			