


План 2-го этажа. Система вентиляции
М 1:100

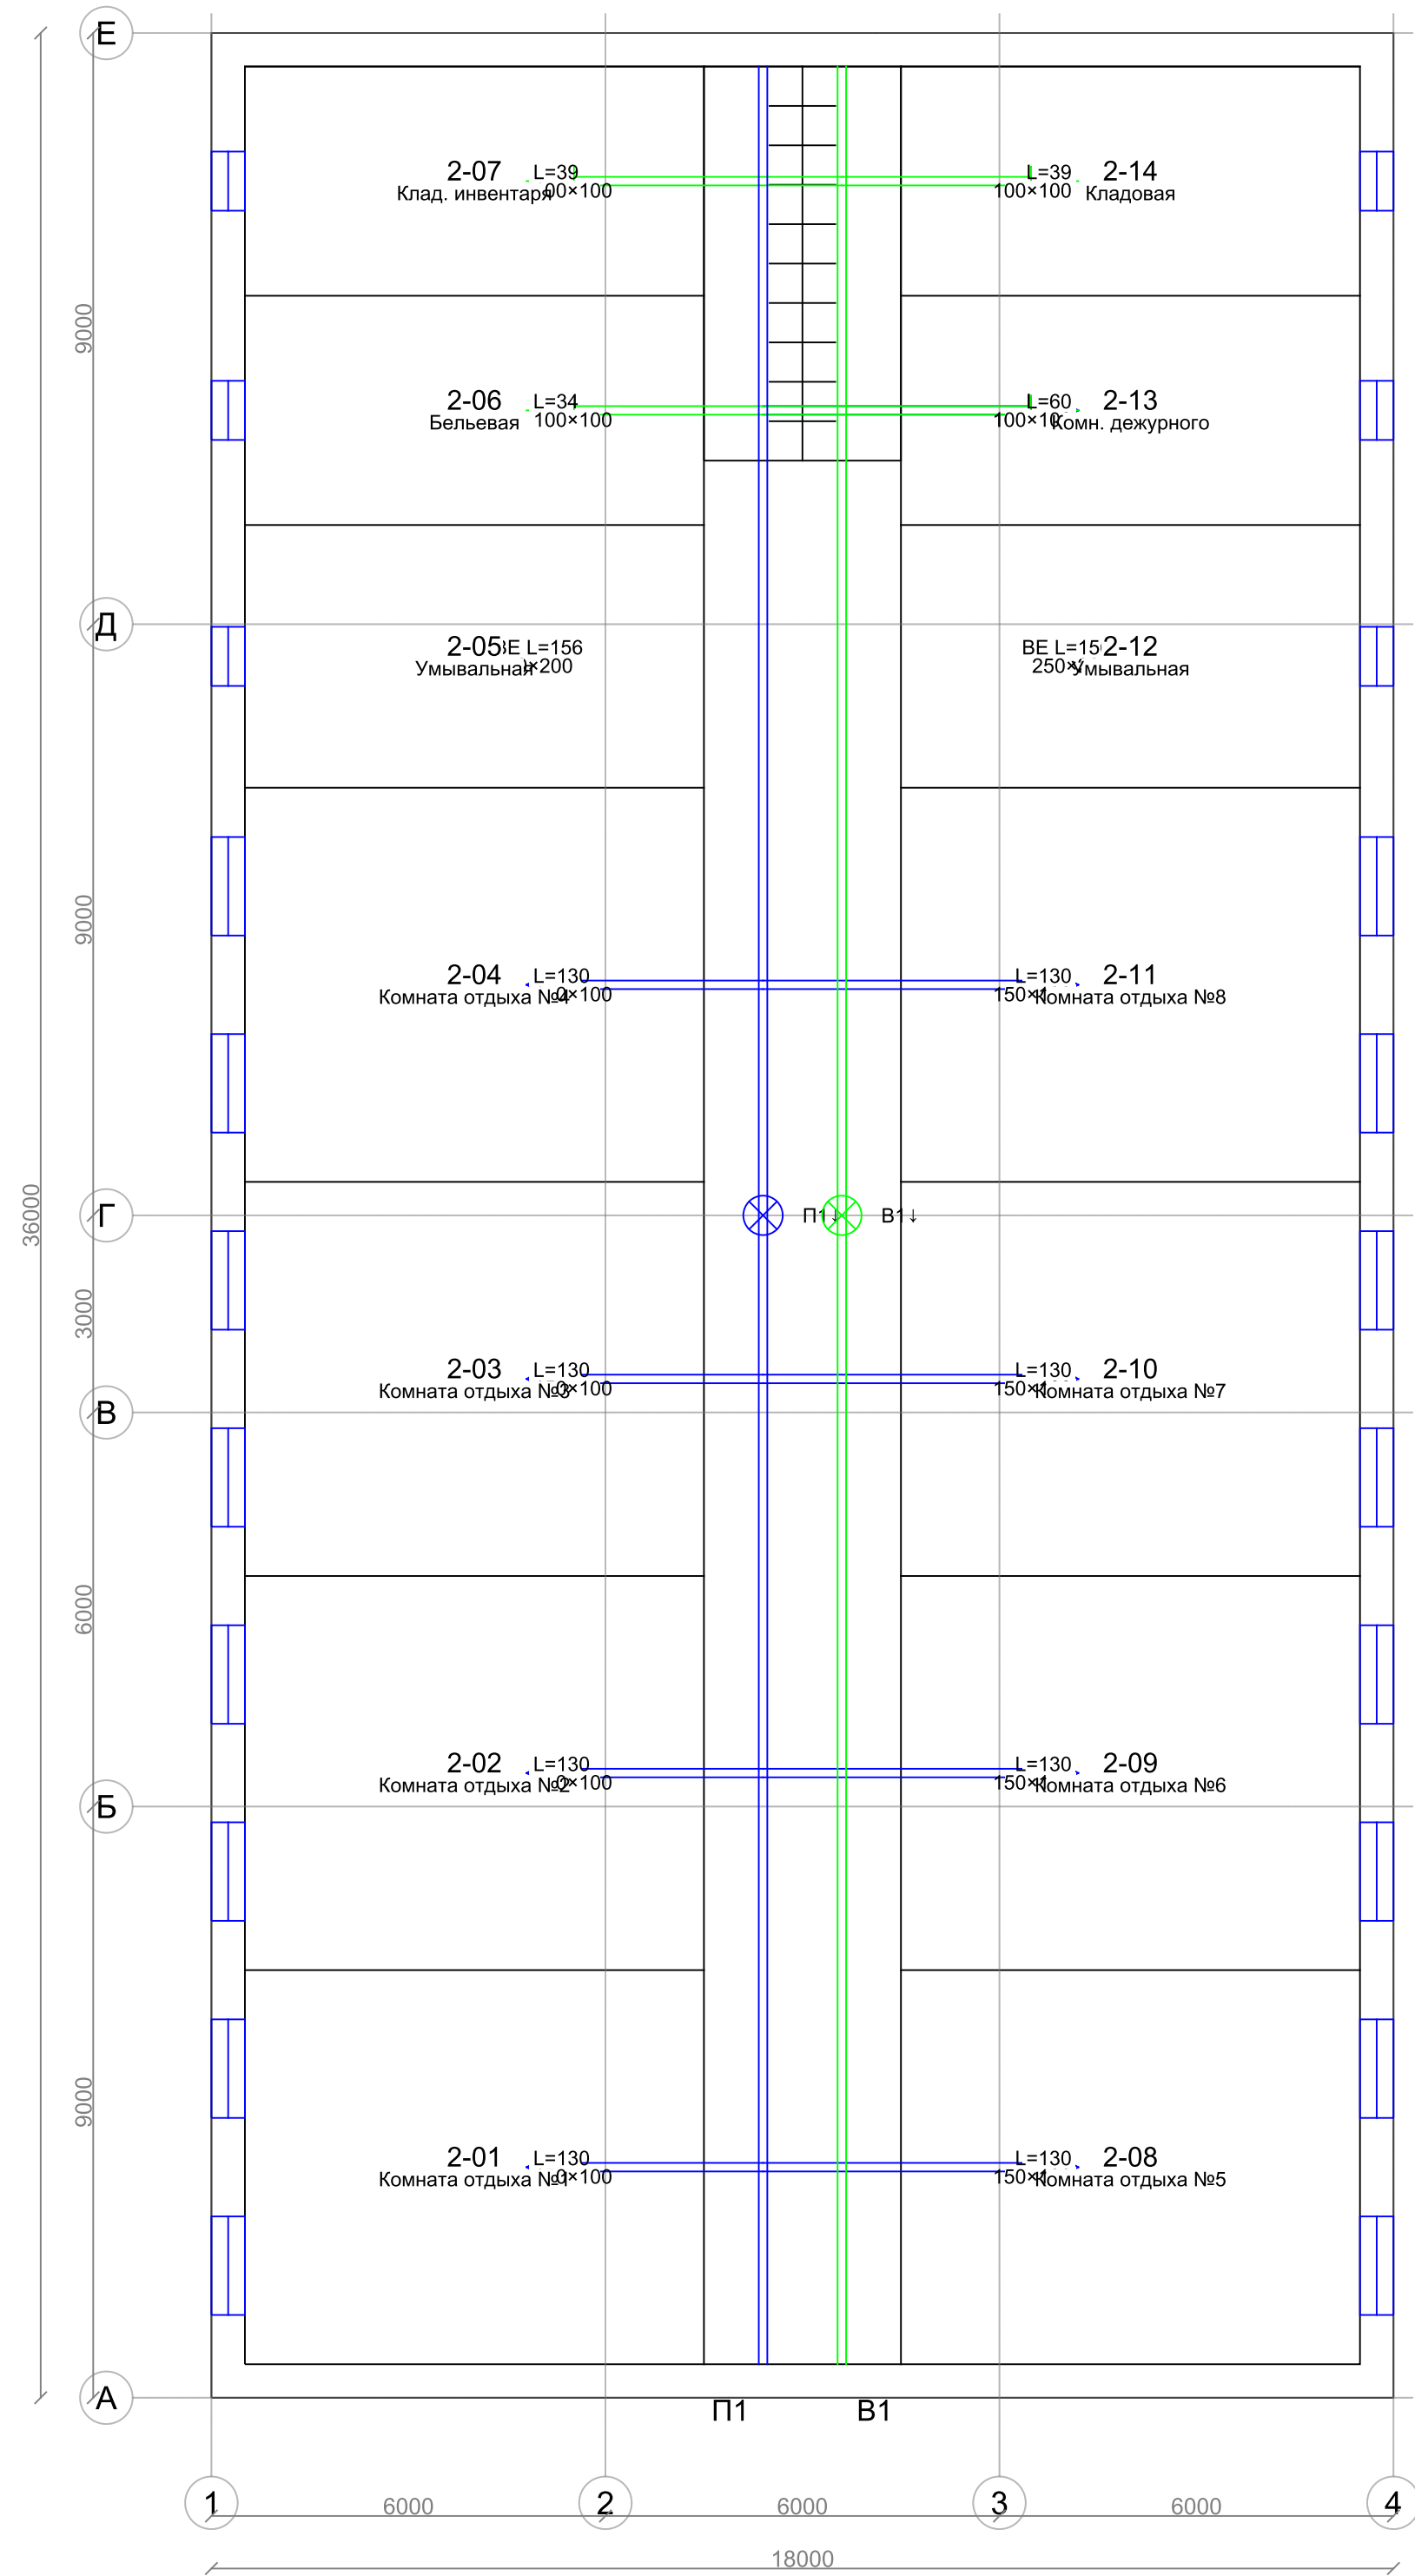

Примечания

- Вентиляция приточно-вытяжная с механическим и естественным побуждением (СП 60.13330.2020, СП 44.13330.2011).
- П1 — приток 3040 м³/ч, t_прит = +18 °С, Breezart 3700 Lux 52,5 (калорифер 52,5 кВт).
- В1 — мех. вытяжка 1180 м³/ч, Systemair KT 50-25-4.
- ВЕ — естеств. вытяжка из умывальных 2-05/2-12 (по 156 м³/ч); санблок и установки — лист 3.
- Воздуховоды стальные; сечения а×в даны у решёток.
- Размеры на чертеже — в мм, расходы L — в м³/ч.

Экспликация помещений

№	Наименование	Размеры, м	S, м²
2-01	Комната отдыха №1	6×6,99	41,9
2-02	Комната отдыха №2	6×6,99	41,9
2-03	Комната отдыха №3	6×6,99	41,9
2-04	Комната отдыха №4	6×6,99	41,9
2-05	Умывальная (левая)	4×6,99	28
2-06	Бельевая	3,49×6,99	24,4
2-07	Кладовая инвентаря	3,49×6,99	24,4
2-08	Комната отдыха №5	6×6,99	41,9
2-09	Комната отдыха №6	6×6,99	41,9
2-10	Комната отдыха №7	6×6,99	41,9
2-11	Комната отдыха №8	6×6,99	41,9
2-12	Умывальная (правая)	4×6,99	28
2-13	Комната дежурного персонала	3,49×6,99	24,4
2-14	Кладовая	3,49×6,99	24,4
2-15	Коридор, лестничная клетка	34,98×3	104,9

Условные обозначения

	П1 — воздуховод приточный (синий)
	В1 — воздуховод вытяжной мех. (зелёный)
	ВЕ — канал естеств. вытяжки (жёлт., штрих.)
	Решётка приточная (стрелка в помещ.)
	Решётка вытяжная (стрелка к каналу)
	Приточная установка Breezart 3700 Lux
	Вытяжной вентилятор Systemair KT 50-25-4
	Стояк (транзит П1/В1 между этажами)

Бытовой корпус базы отдыха «Дубрава» Система вентиляции. План 2-го этажа						МИВУ.080301.018-ОВ		
Изм.		Лист	№ докум.	Подп.	Дата			
Разраб.			Лукашин А. О.			М 1:100		
Руковод.			Полуляк Г.П.					
Н. контр.			—					
Утв.			Шарапов Р.В.					
						Стадия — ВКР		
						2026 г.		
						Муромский институт (филиал) ВлГУ кафедра ТБ		