


Принципиальная схема котельной (без масштаба)



АксонOMETрическая схема системы отопления (фронтальная изометрия)

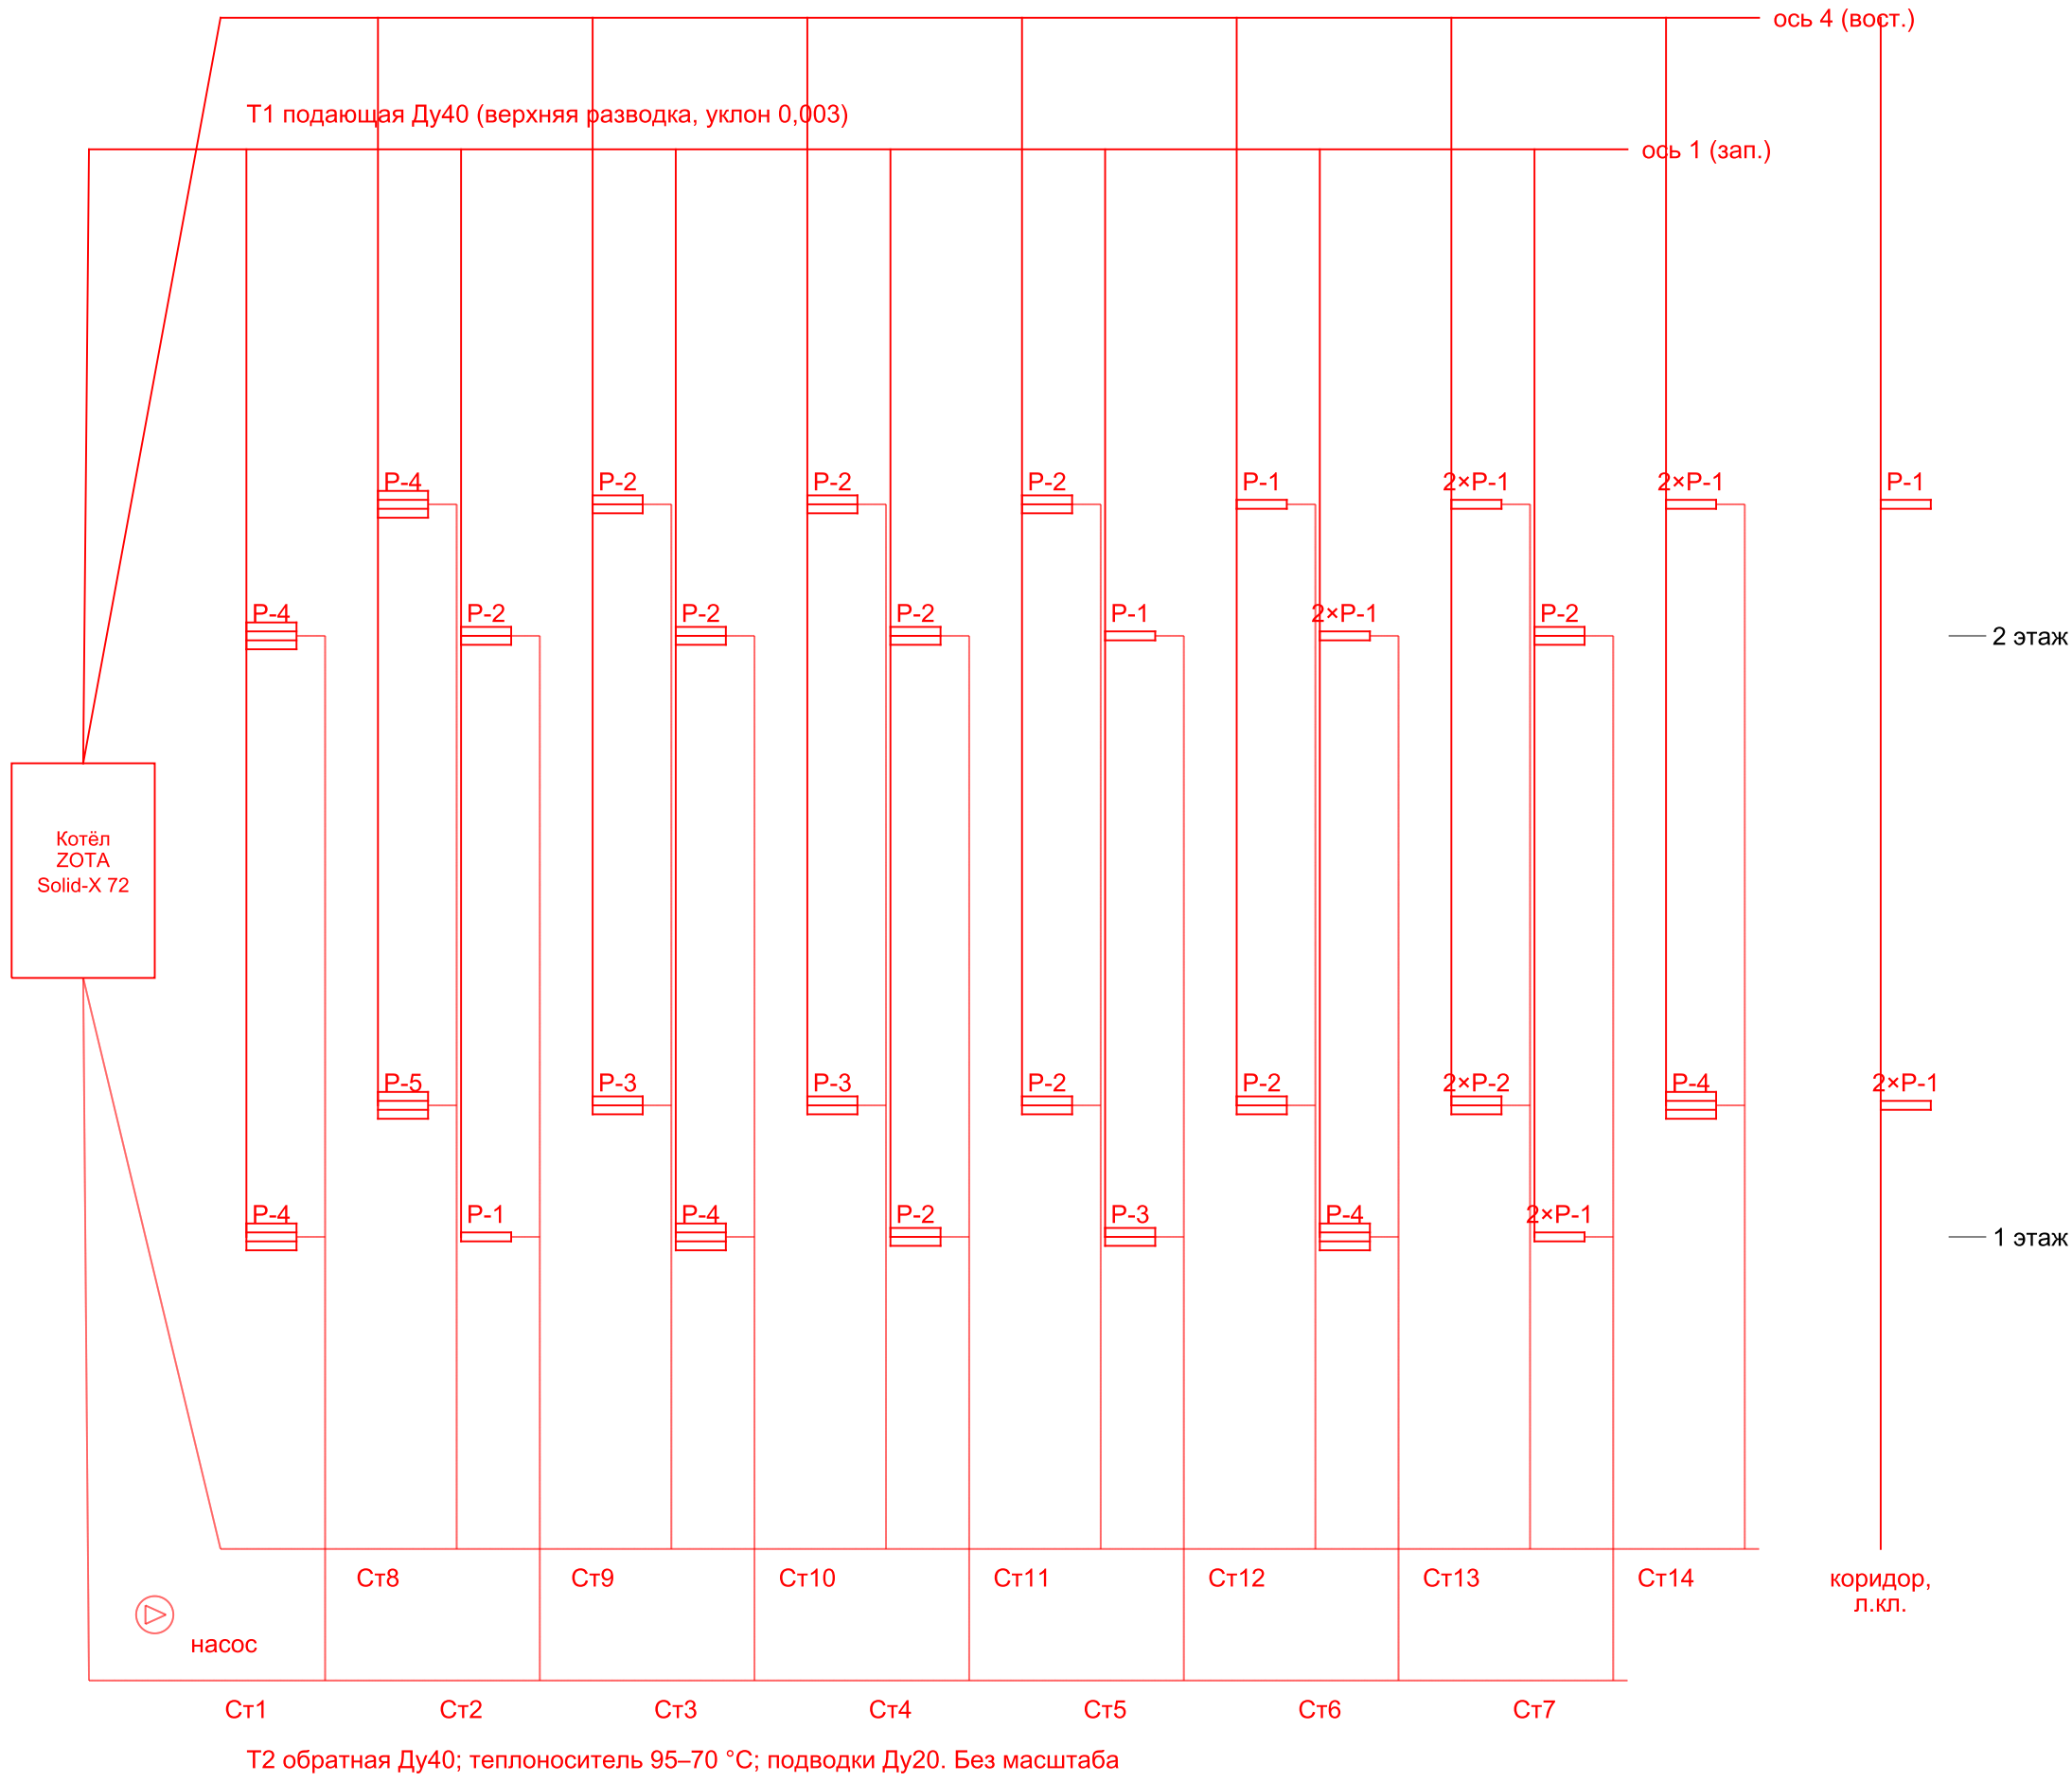

Спецификация оборудования котельной

Поз.	Наименование	Марка / параметр	Кол.
1	Электркотёл	ZOTA Solid-X 72	1
2	Циркуляционный насос	Grundfos UPS 25-60	1
3	Расширительный бак	Reflex N 500	1
4	Группа безопасности	клапан 3 бар, возд., маном.	1
5	Фильтр-грязевик	косой сетчатый Ду25	1
6	Узел подпитки	от водопр. Ø20, кран+обр.кл.	1
7	Запорная арматура	краны шаровые Ду20...40	компл.

Ведомость отопительных приборов (регистры Ø108×4, ГОСТ 10704)

Марка	Труб п×L, м	Q _t , Вт	Кол.	L труб, м
P-1	2×3,0	1366	14	84,0
P-2	3×3,0	1948	12	108,0
P-3	3×4,0	2598	3	36,0
P-4	4×4,0	3296	6	96,0
P-5	4×5,0	4120	1	20,0
Итого регистров Ø108×4			36	344,0

Бытовой корпус базы отдыха «Дубрава» Система отопления. Аксонометрическая схема. Схема котельной						МИВУ.080301.018-ОВ		
						Стадия	Лист	Листов
						ВКР	5	6
Изм.	Лист	№ докум.	Подп.	Дата	Б/М	Муромский институт (филиал) ВлГУ кафедра ТБ		
Разраб.	Лукашин А. О.	Полуляк Г.П.						
Руковод.	—							
Н. контр.	Шарапов Р.В.							
Утв.					Стадия — ВКР			
					2026 г.			