



АксонOMETрическая схема приточной системы П1

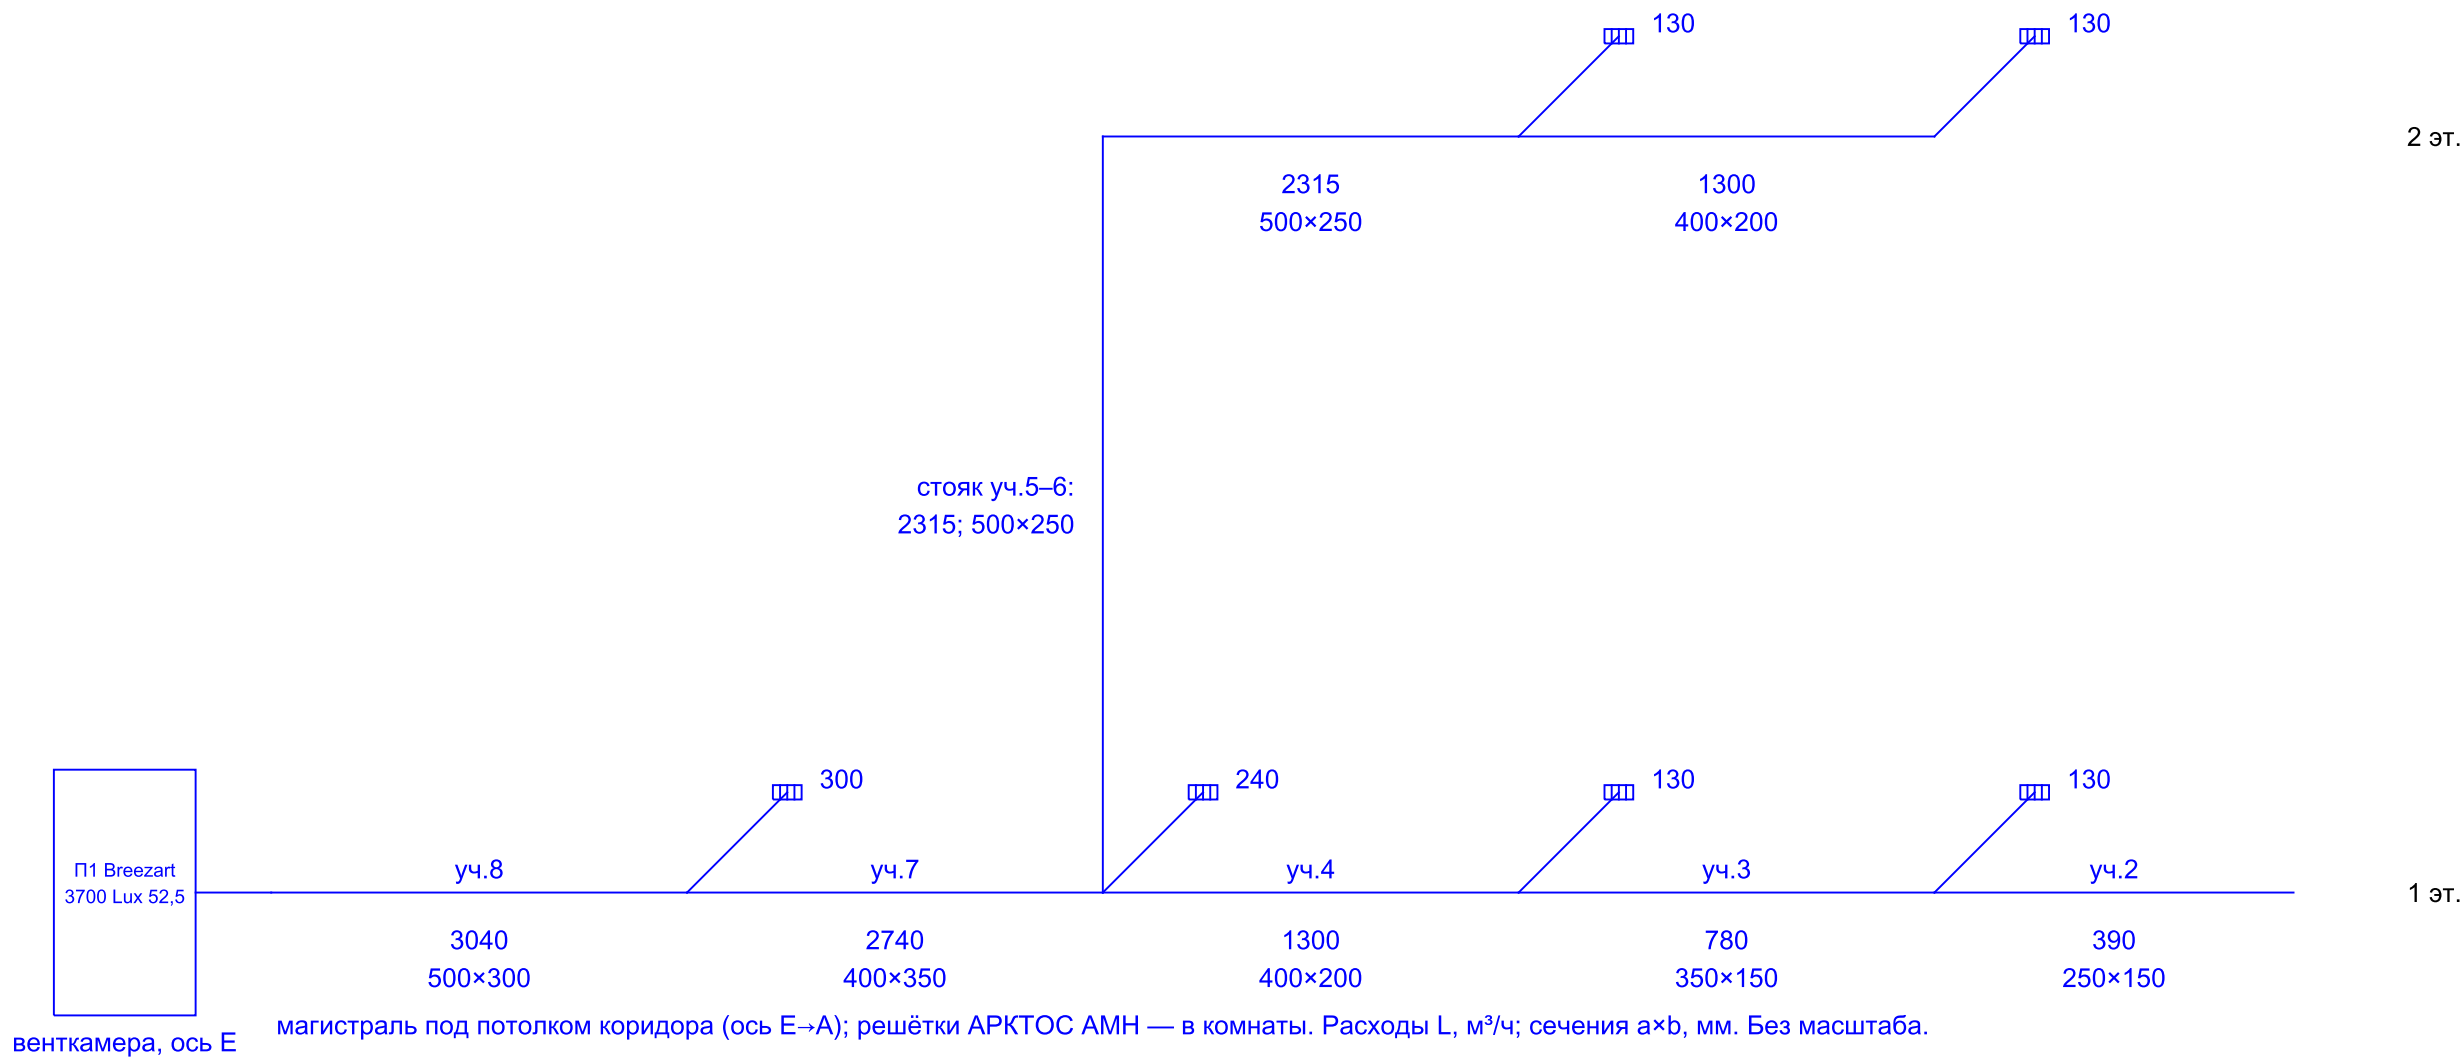

Спецификация вентиляционного оборудования

Поз.	Наименование	Марка / параметр	Кол.
1	Приточная установка П1	Breezart 3700 Lux 52,5	1
2	Электродокалифери (встроени)	до 52,5 кВт, 380 В	1
3	Фильтр (встроени)	класс G4	1
4	Вытяжной вентилятор В1	Systemair КТ 50-25-4	1
5	Воздухораспределители	решётки АРКТОС АМН/АМР	компл.

АксонOMETрическая схема вытяжной системы В1

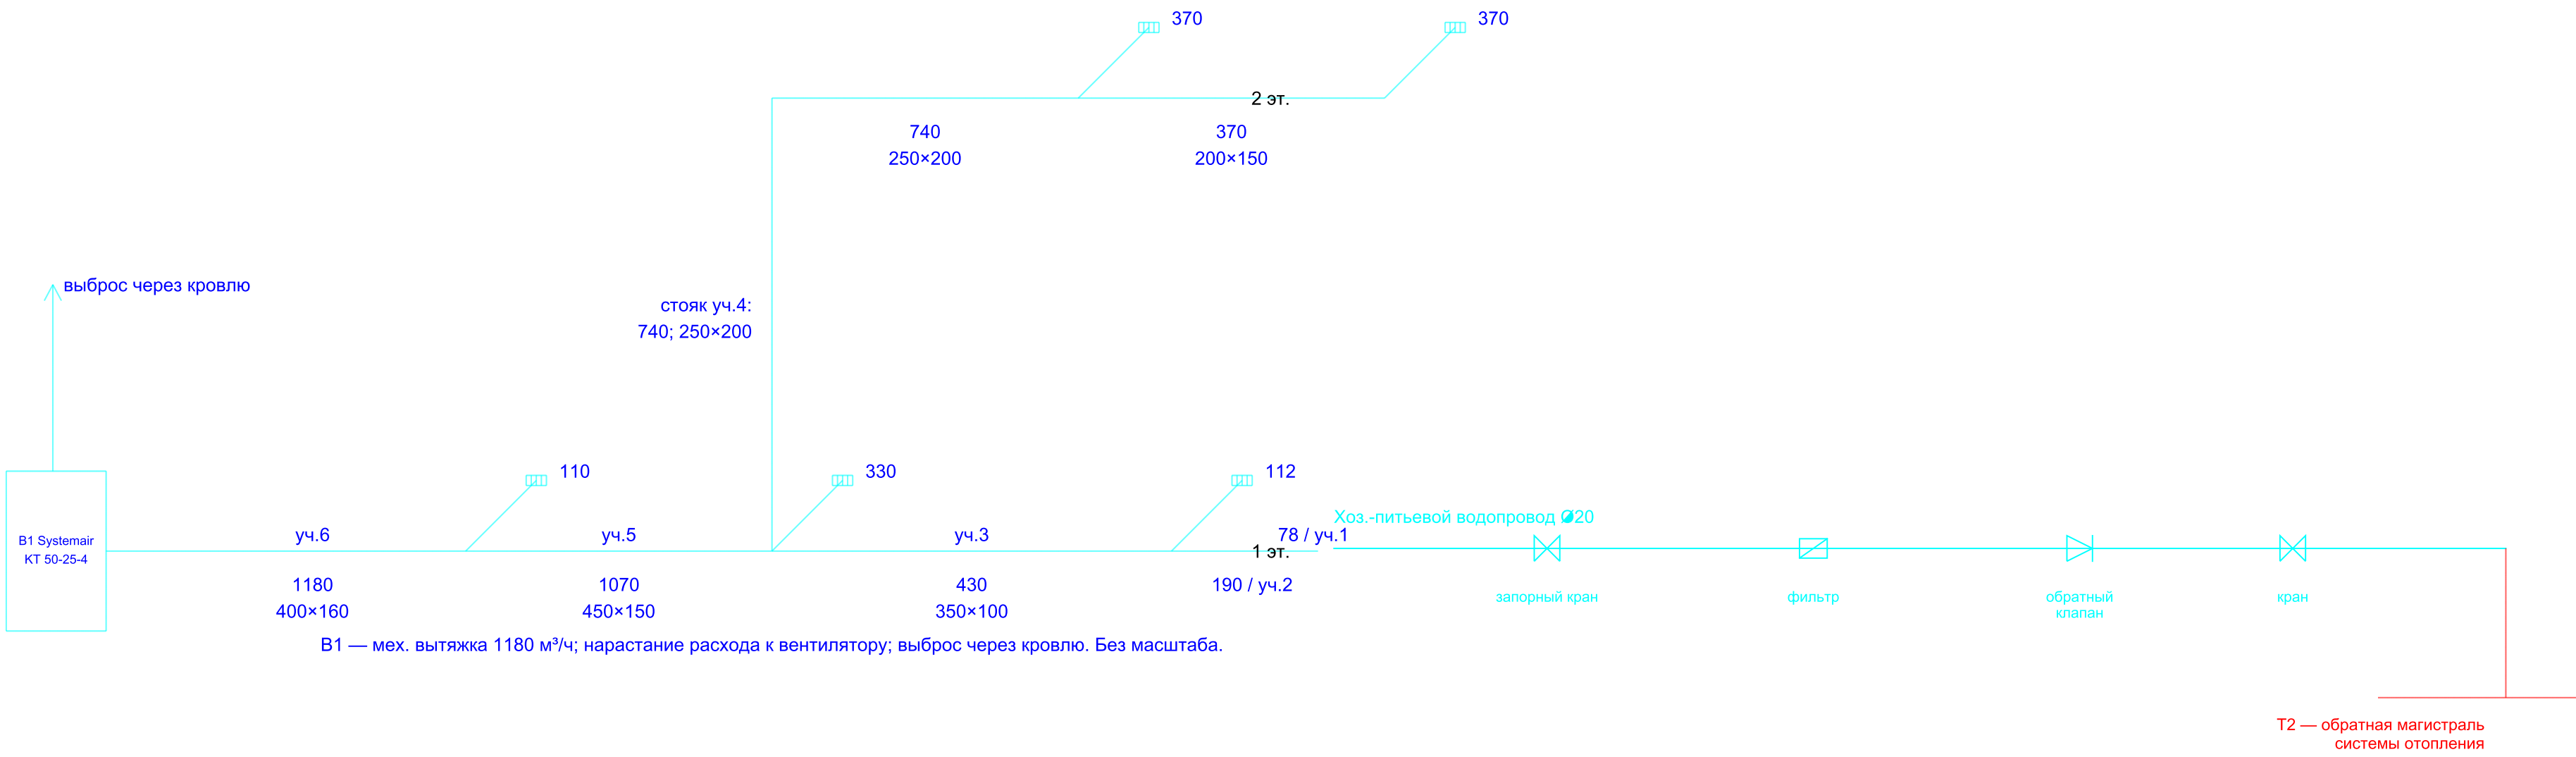

Узел ХВС / подпитки системы отопления (без масштаба)

Бытовой корпус базы отдыха «Дубрава» Система вентиляции. Аксонометрическая схема. Узел ХВС						МИВУ.080301.018-ОВ		
						Стадия	Лист	Листов
						ВКР	6	6
Изм.	Лист	№ докум.	Подп.	Дата	Б/М	Муромский институт (филиал) ВлГУ кафедра ТБ		
Разраб.		Лукашин А. О.						
Руковод.		Полуляк Г.П.						
Н. контр.		—						
Утв.		Шарапов Р.В.			Стадия — ВКР			
					2026 г.			