


План 2-го этажа. Система отопления
М 1:100

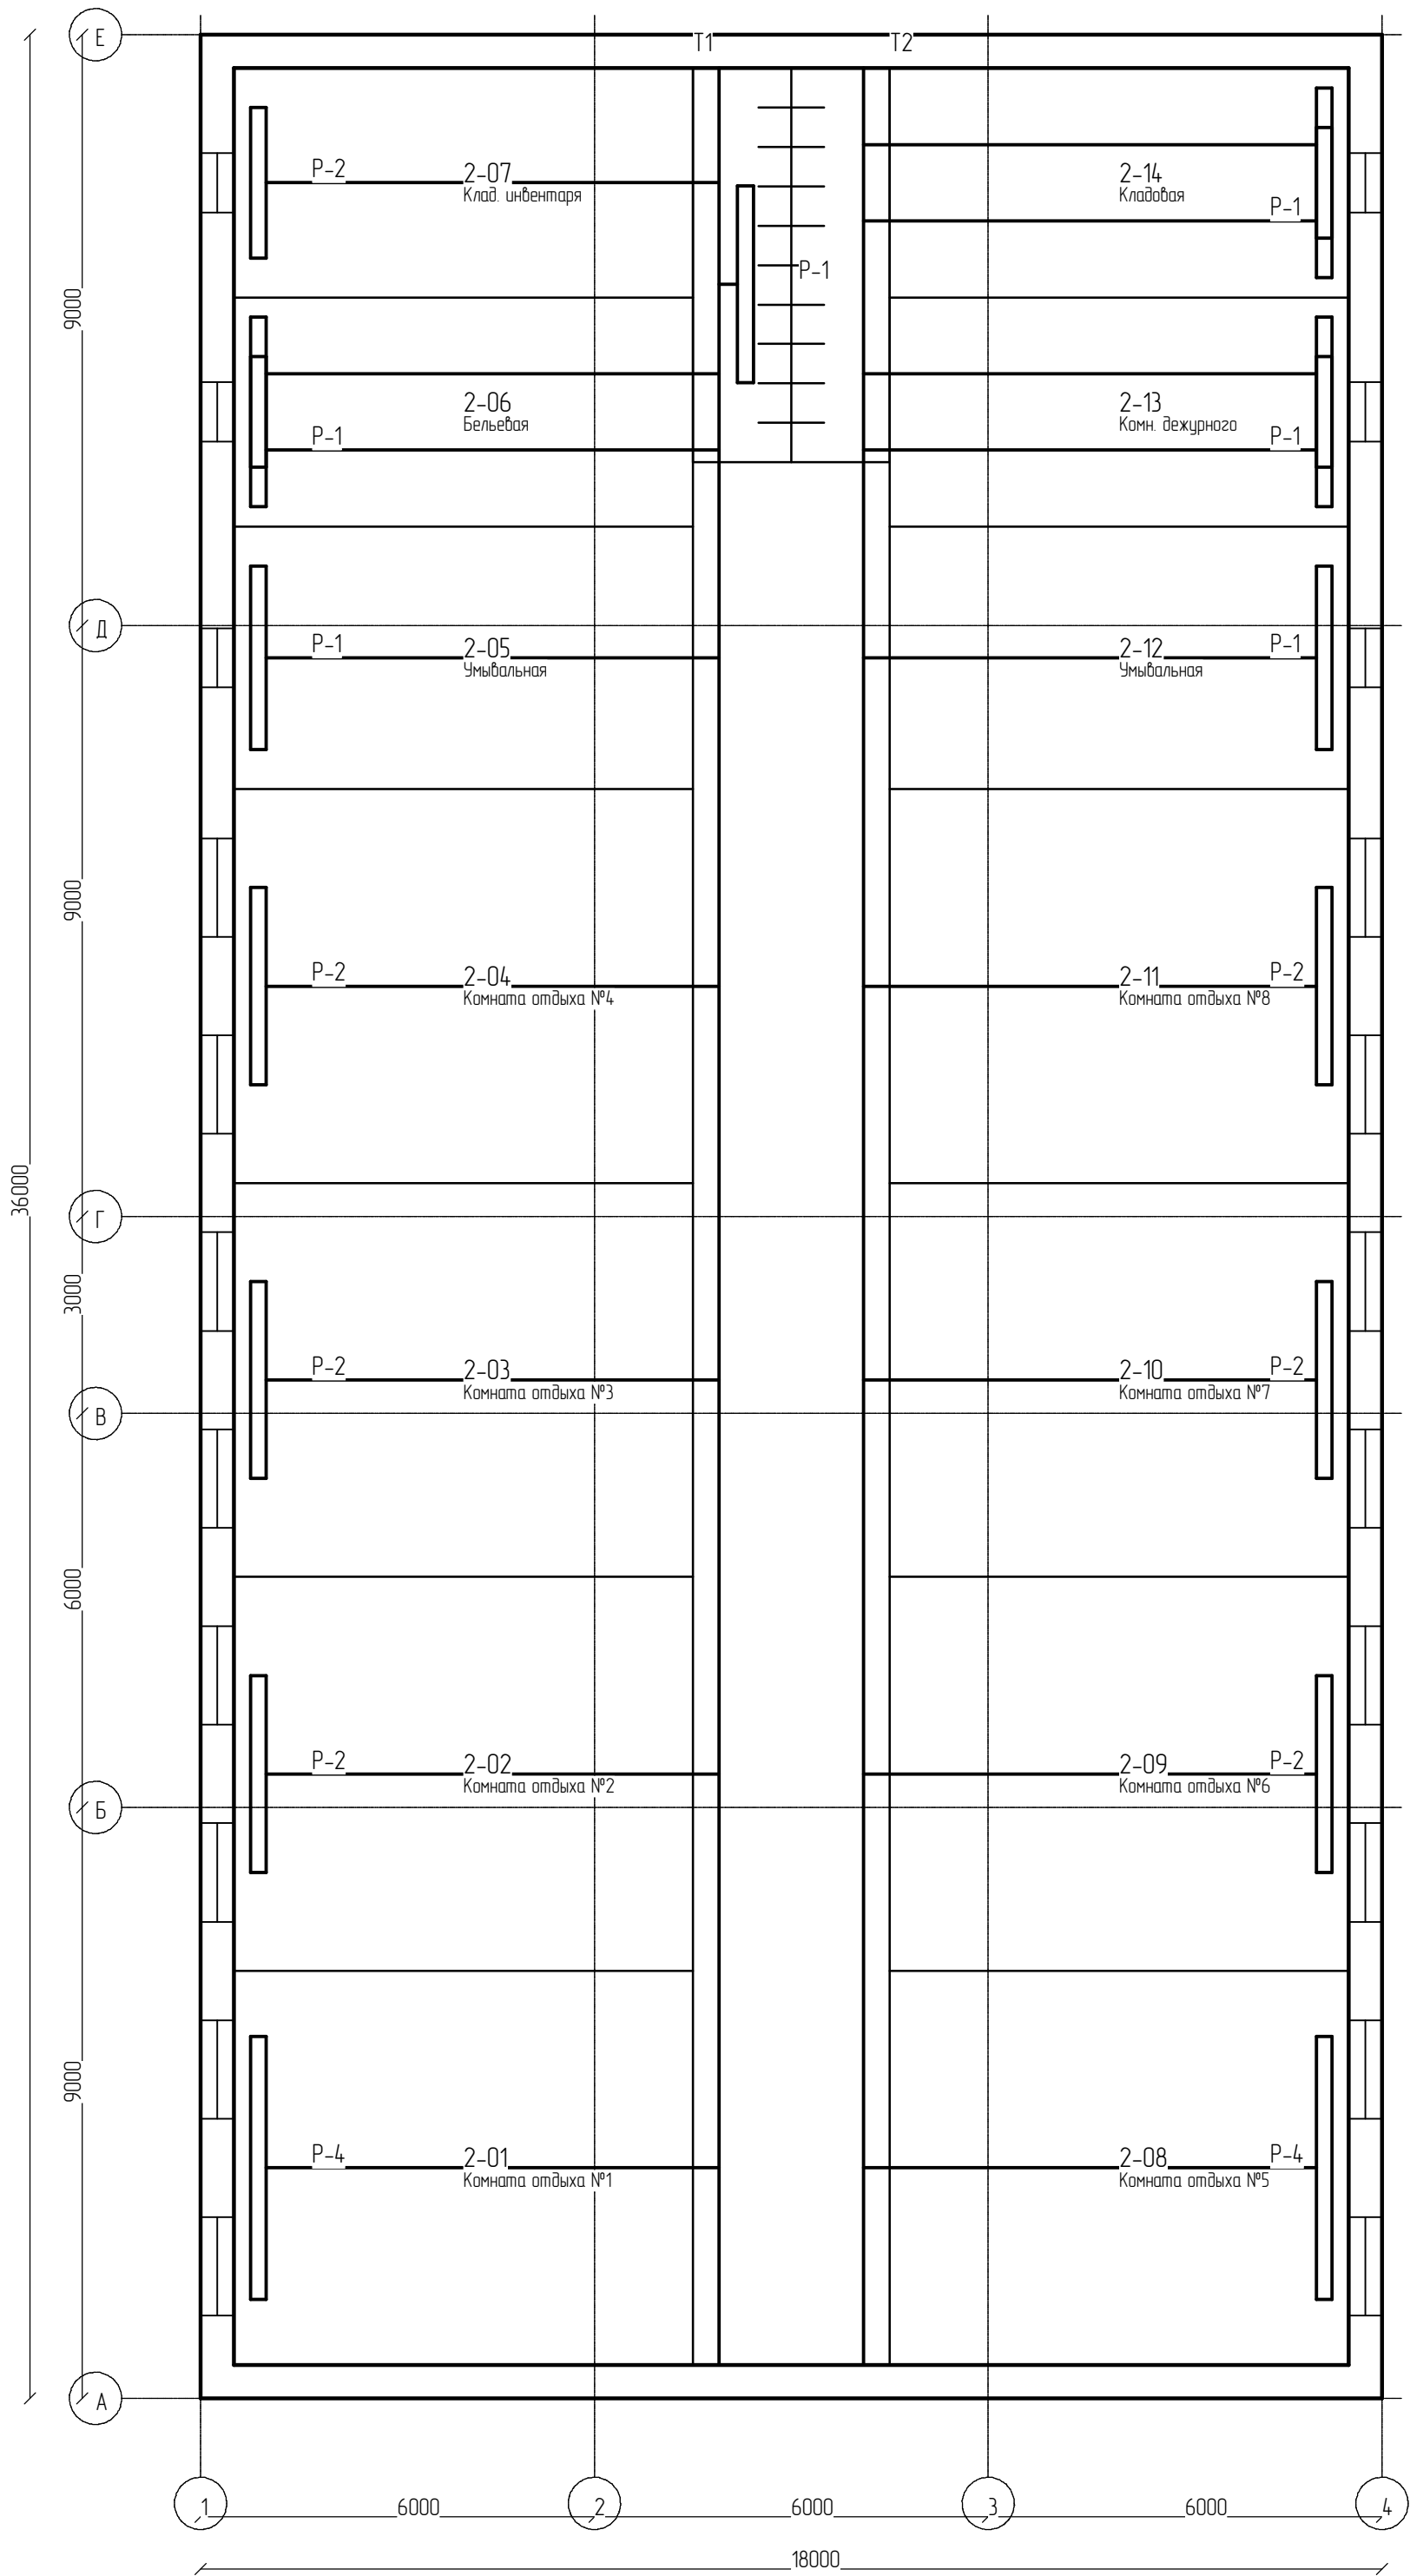

Экспликация помещений 12 этажа			
№	Наименование	площ. м	С. м²
2-01	Комната отдыха №1	6,6,99	419
2-02	Комната отдыха №2	6,6,99	419
2-03	Комната отдыха №3	6,6,99	419
2-04	Комната отдыха №4	6,6,99	419
2-05	Умывальник	4,6,99	28
2-06	Бельежная	31,9,4,99	24,4
2-07	Класс инвентаря	31,9,4,99	24,4
2-08	Комната отдыха №5	6,6,99	419
2-09	Комната отдыха №6	6,6,99	419
2-10	Комната отдыха №7	6,6,99	419
2-11	Комната отдыха №8	6,6,99	419
2-12	Умывальник	4,6,99	28
2-13	Канн. дежурного	31,9,4,99	24,4
2-14	Кладовая	31,9,4,99	24,4
2-15	Коридор, лестничная клетка	36,98,3	104,9

Примечания

1. Система отопления двухтрубная с верхней разводкой.
2. Теплоноситель – вода 95-70 °С, t.c.p. = 82,5 °С.
3. Отопительные приборы – регистры из стальных труб Ø108-4 (ГОСТ 10704), окраска масляной краской в 2 слоя.
4. Источник теплоты – электродкотел ZOTA Solid-X 72 (72 кВт), помещение электродкотельной 1-08.
5. Размеры на чертеже – в мм, отметки – в м.

Копировал _____ Формат А1