


АксонOMETрическая схема системы отопления

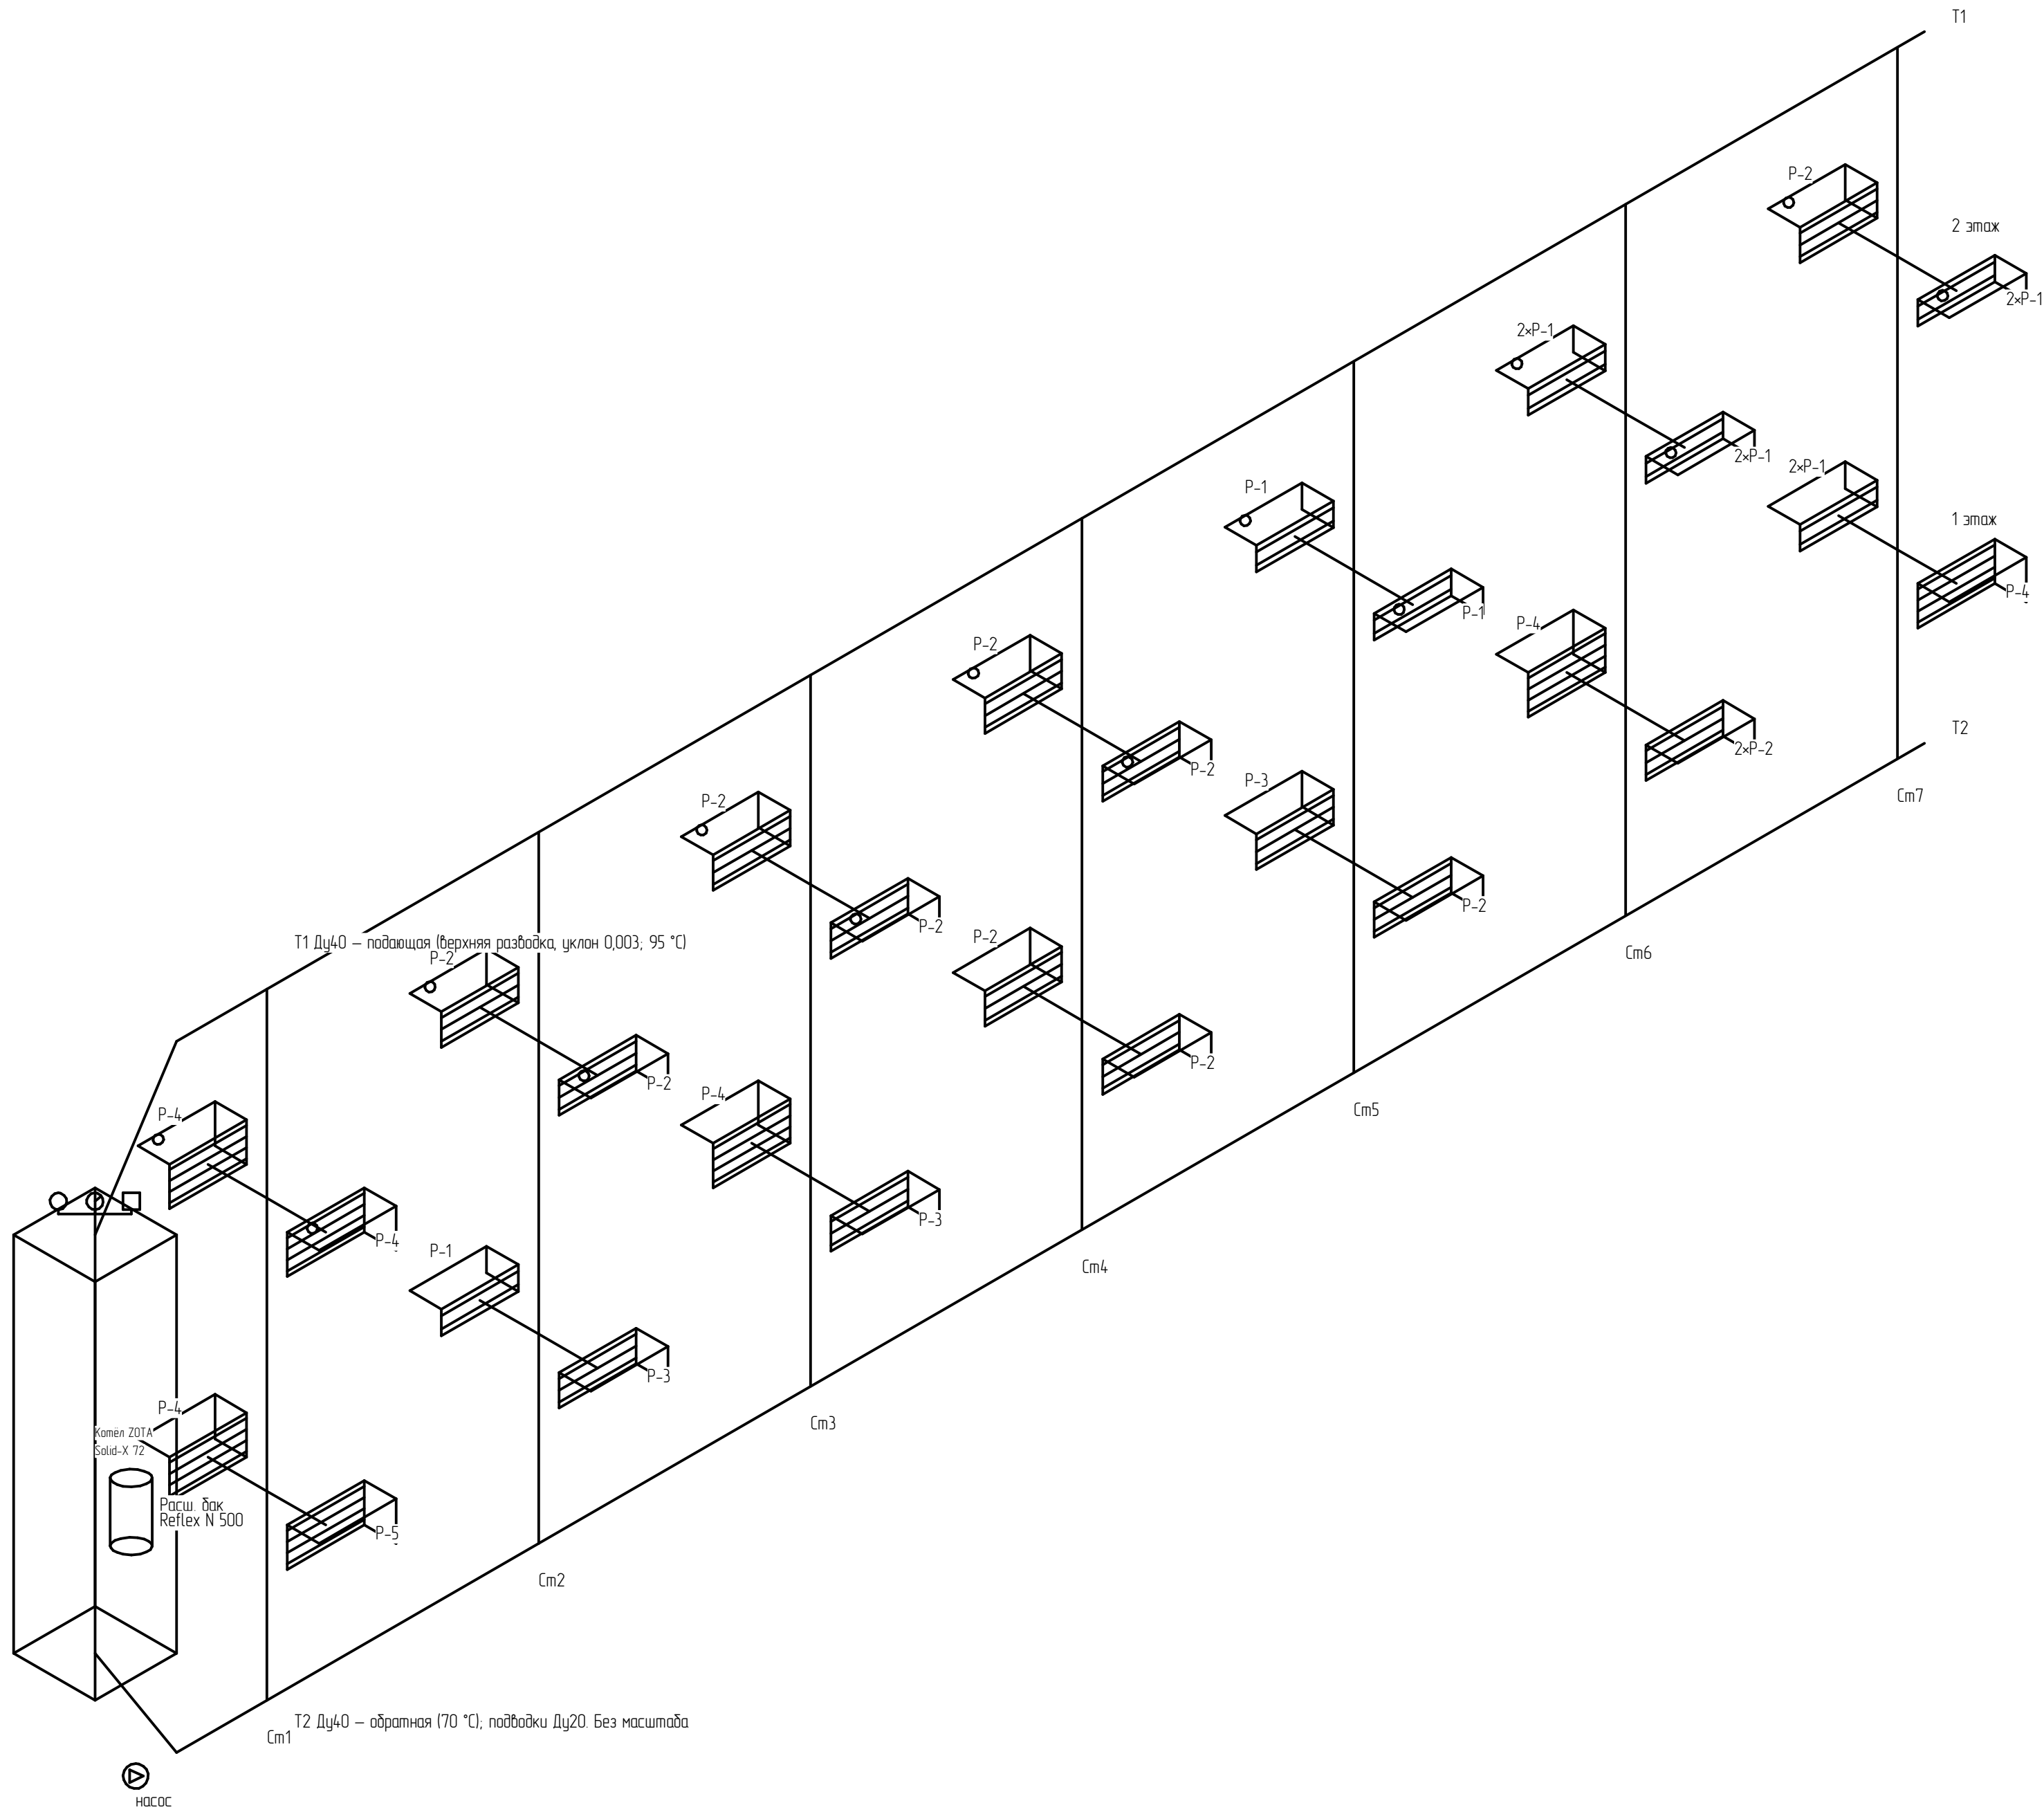

Ведомость отопительных приборов (регистры Ø108×4, ГОСТ 10704)

Марка	Труб п-л, м	Q , Вт	Кол.	Л. труб, м
P-1 2×3,0		1366	14	84,0
P-2 3×3,0		1948	12	108,0
P-3 3×4,0		2598	3	36,0
P-4 4×4,0		3296	6	96,0
P-5 4×5,0		4120	1	20,0
Итого регистров Ø108×4			36	344,0

Примечания

- Система двухтрубная тупиковая с верхней разводкой; теплоноситель – вода 95–70 °C, t_{ср} = 82,5 °C.
- Приборы – регистры из гладких труб Ø108×4 (ГОСТ 10704), марки P-1..P-5; всего 36 шт, 344 п.м.
- Магистроли Т1/Т2 Ду40, подводы к приборам Ду20, стояки – по оси коридора, выпуски – к приборам этажей.
- Схема выполнена без масштаба, размеры – в мм.

МИВЧ.080301.018 АС1					Система отопления			Лист	Масса	Масштаб
Изм.	Лист	№ док.	Подп.	Дата	Разраб.	Лыкашин А.О.				
					Проб.	Полулях Г.И.				
					Т.контр.			Лист	Листов	1
Н.контр.	Передущий Р.В.				Утв.	Шарапов Р.В.		МИ ВЛГУ		
					СТ-122			Копировал		
								Формат А1		