


МИВУ.080301.018 Г5

Схема подключения холодного водоснабжения (узел ввода и подпитки системы отопления). Без масштаба

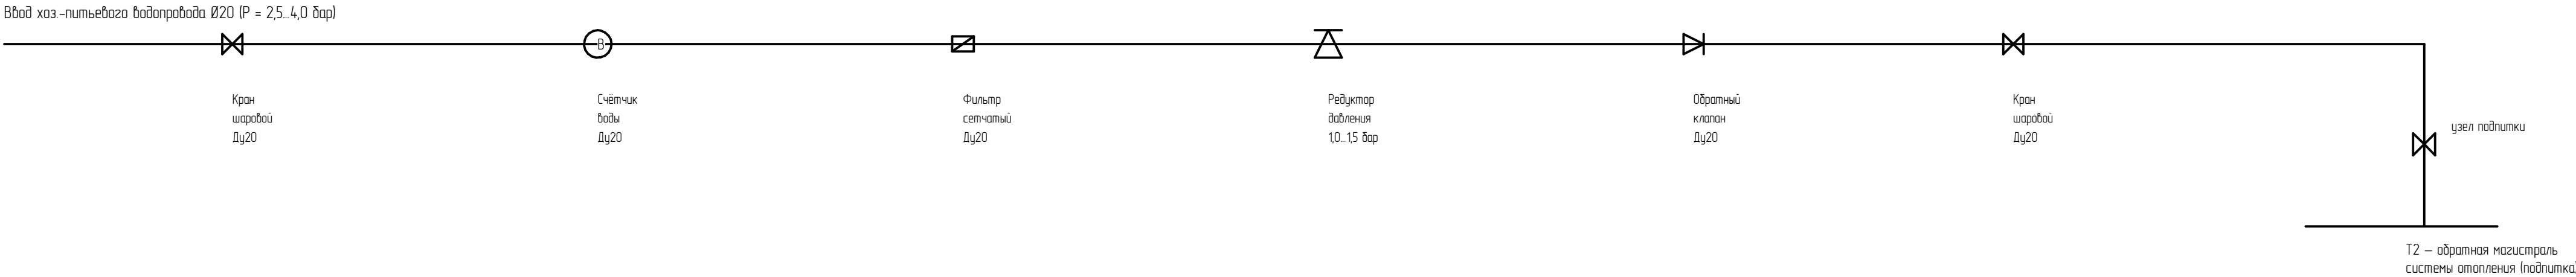

Спецификация узла ХВС / подпитки

Поз.	Наименование	Параметр / кол.
1	Кран шаровый Ду20	2 шт
2	Счетчик воды крыльчатый	Ду20, 1 шт
3	Фильтр сетчатый кокой	Ду20, 1 шт
4	Редуктор давления	Ду20, 10..15 бар
5	Клапан обратный пружинный	Ду20, 1 шт
6	Трубопровод ХВС	сталь/ППР Ø20

Примечания

- Подпитка системы отопления (V - 2930 л) – из хоз.-питьевого водопровода Ø20 через редуктор и обратный клапан.
- Редуктор настроен на давление выше статического давления системы (Р = 10 бар при остывании теплоносителя).
- Обратный клапан исключает попадание теплоносителя в ХВС.
- Давление сети ХВС, счётчик и редуктор приняты по типовому инженерному решению (в расчётной части не добавлялись).
- Схема без масштаба, диаметры даны по ГОСТ.

					МИВУ.080301.018 Г5					
Изм	Лист	№ докум	Подп	Дата	Водоснабжение холодное. Схема гидравлическая подключение			Лит	Масса	Масштаб
								Лист	Листов	1
Исх. контр.	Передвиж. РВ	Учб	Шаровый РВ					МИ ВЛГУ СТ-122		