



Аксонометрическая схема приточной системы П1

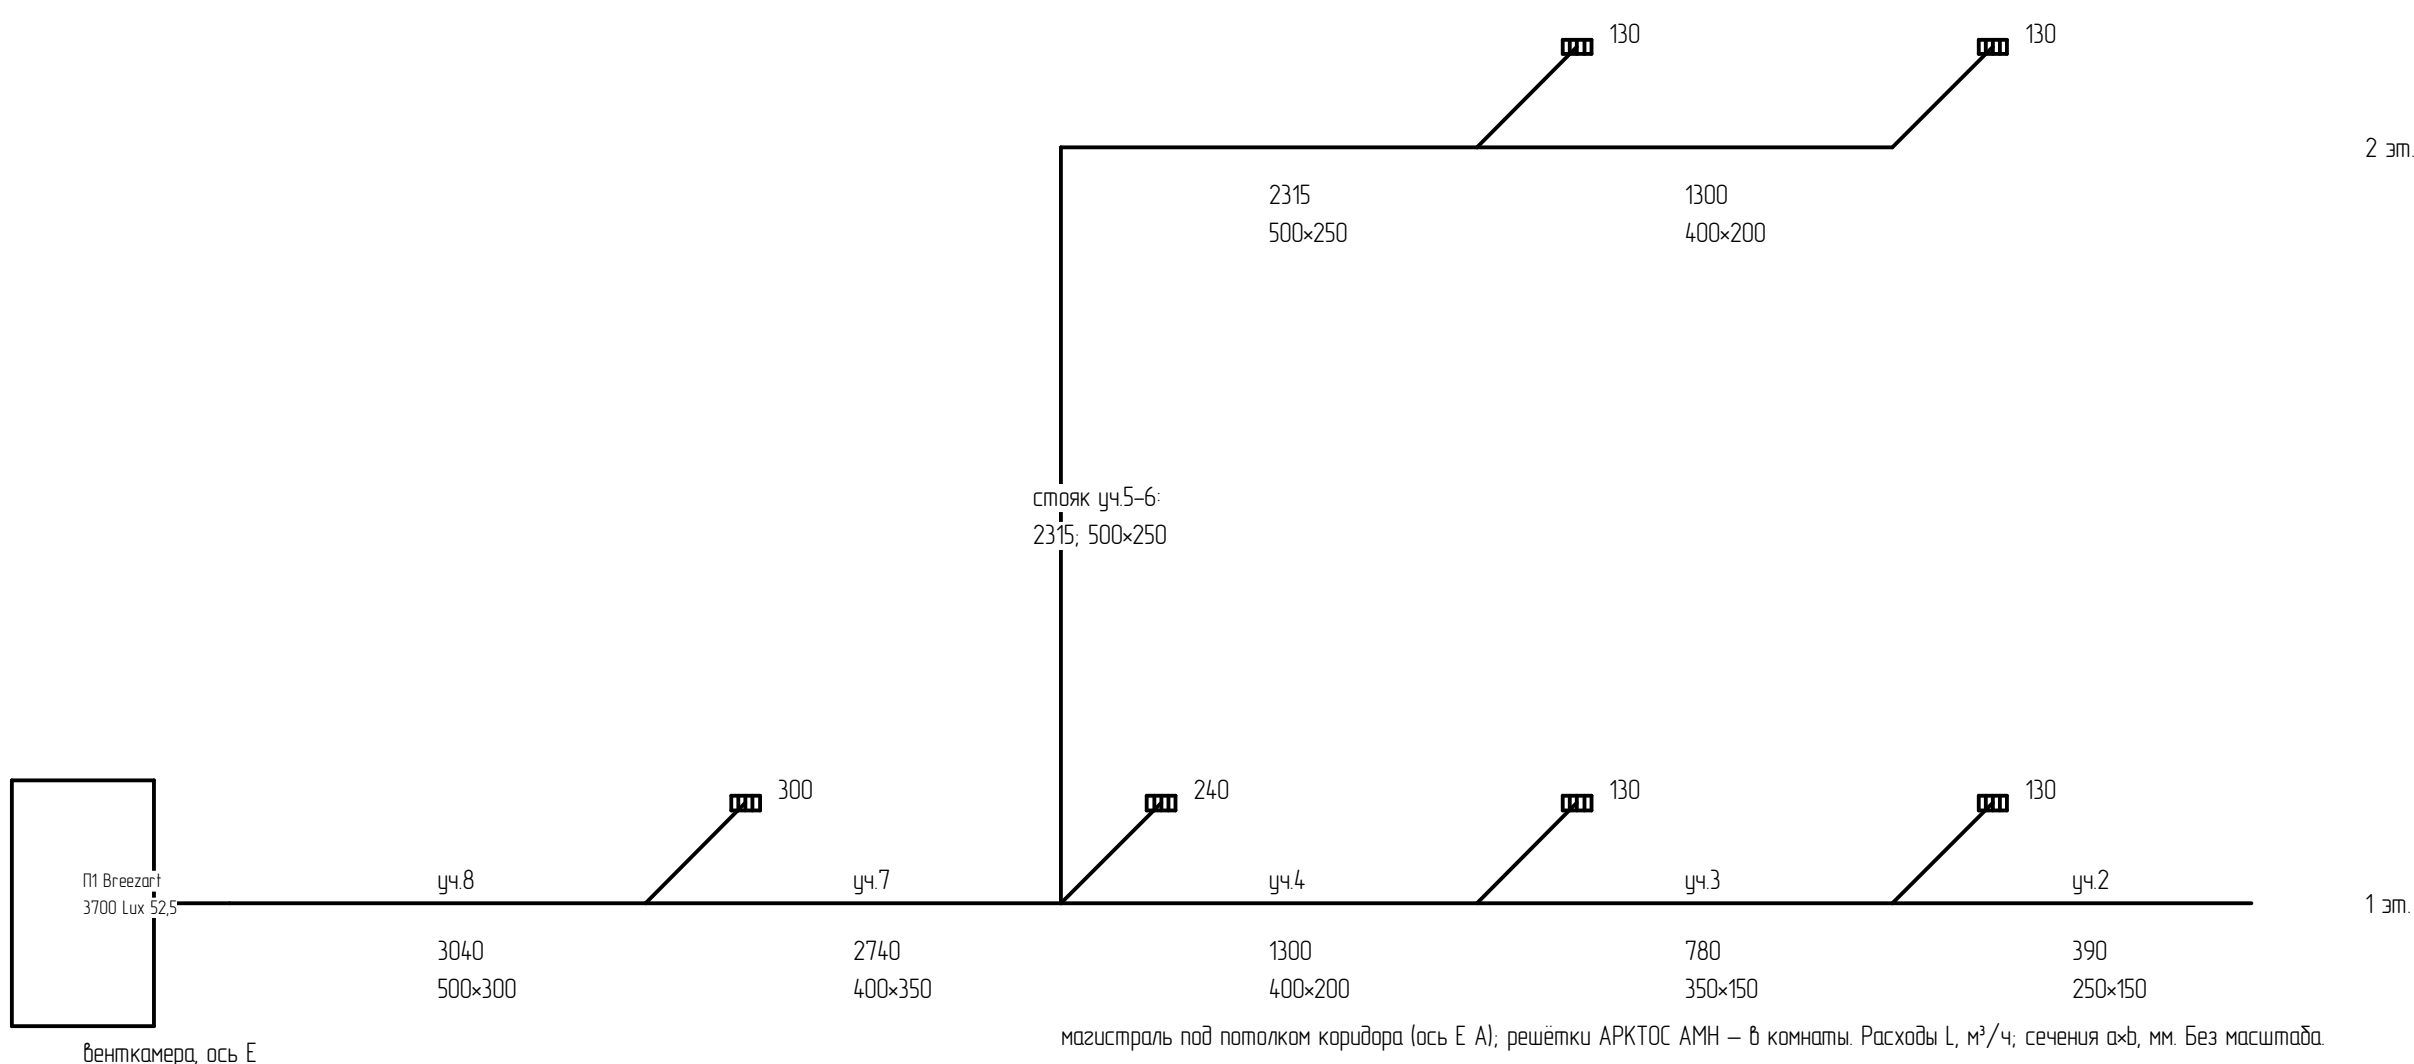

Аксонометрическая схема вытяжной системы В1

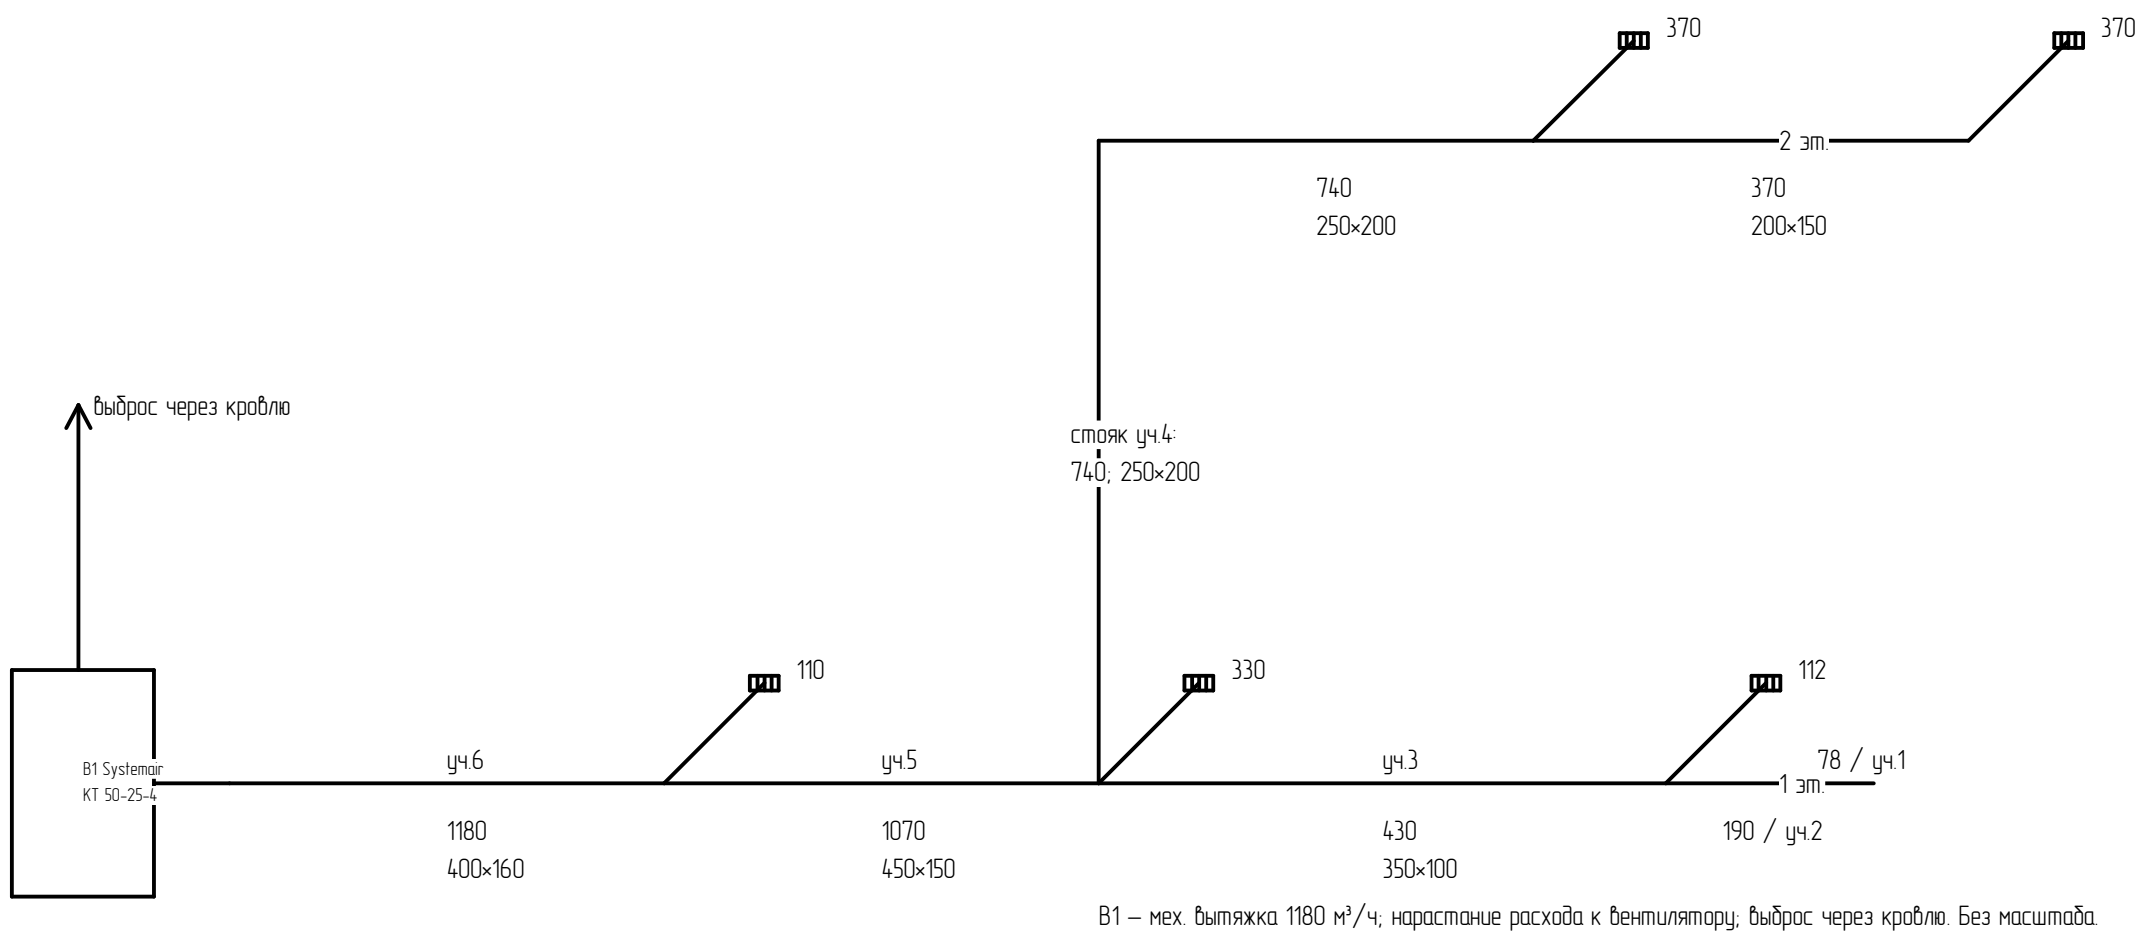

Спецификация вентиляционного оборудования

Поз.	Наименование	Марка / параметр	Кол.
1	Приточная установка П1	Breezart 3700 Lux 525	1
2	Электрокалорифер (встроен)	до 525 кВт, 380 В	1
3	Фильтр (встроен)	класс G4	1
4	Вытяжной вентилятор В1	Systemair KT 50-25-4	1
5	Воздухораспределители	решётки АРКТОС АМН/АМР	компл.

				МИВЧ.080301.018-ОВ			
Изм. Лист	№ докум.	Подп.	Дата	Бытовой корпус дачы «Дубрава» Система вентиляции Аксонометрическая схема	Лист	Масса	Масштаб
Разраб.	Лукашин А.О.				3		1:100
Проб.	Полуха Г.Л.				Лист	Листов	1
Т. контр.							
Н. контр.	Пердусиш Р.В.				МИ ВЛЧ СТ-122		
Утв.	Шарапов Р.В.						