



МВУ.080301.018-0В

План 1-го этажа. Система отопления
М 1:100

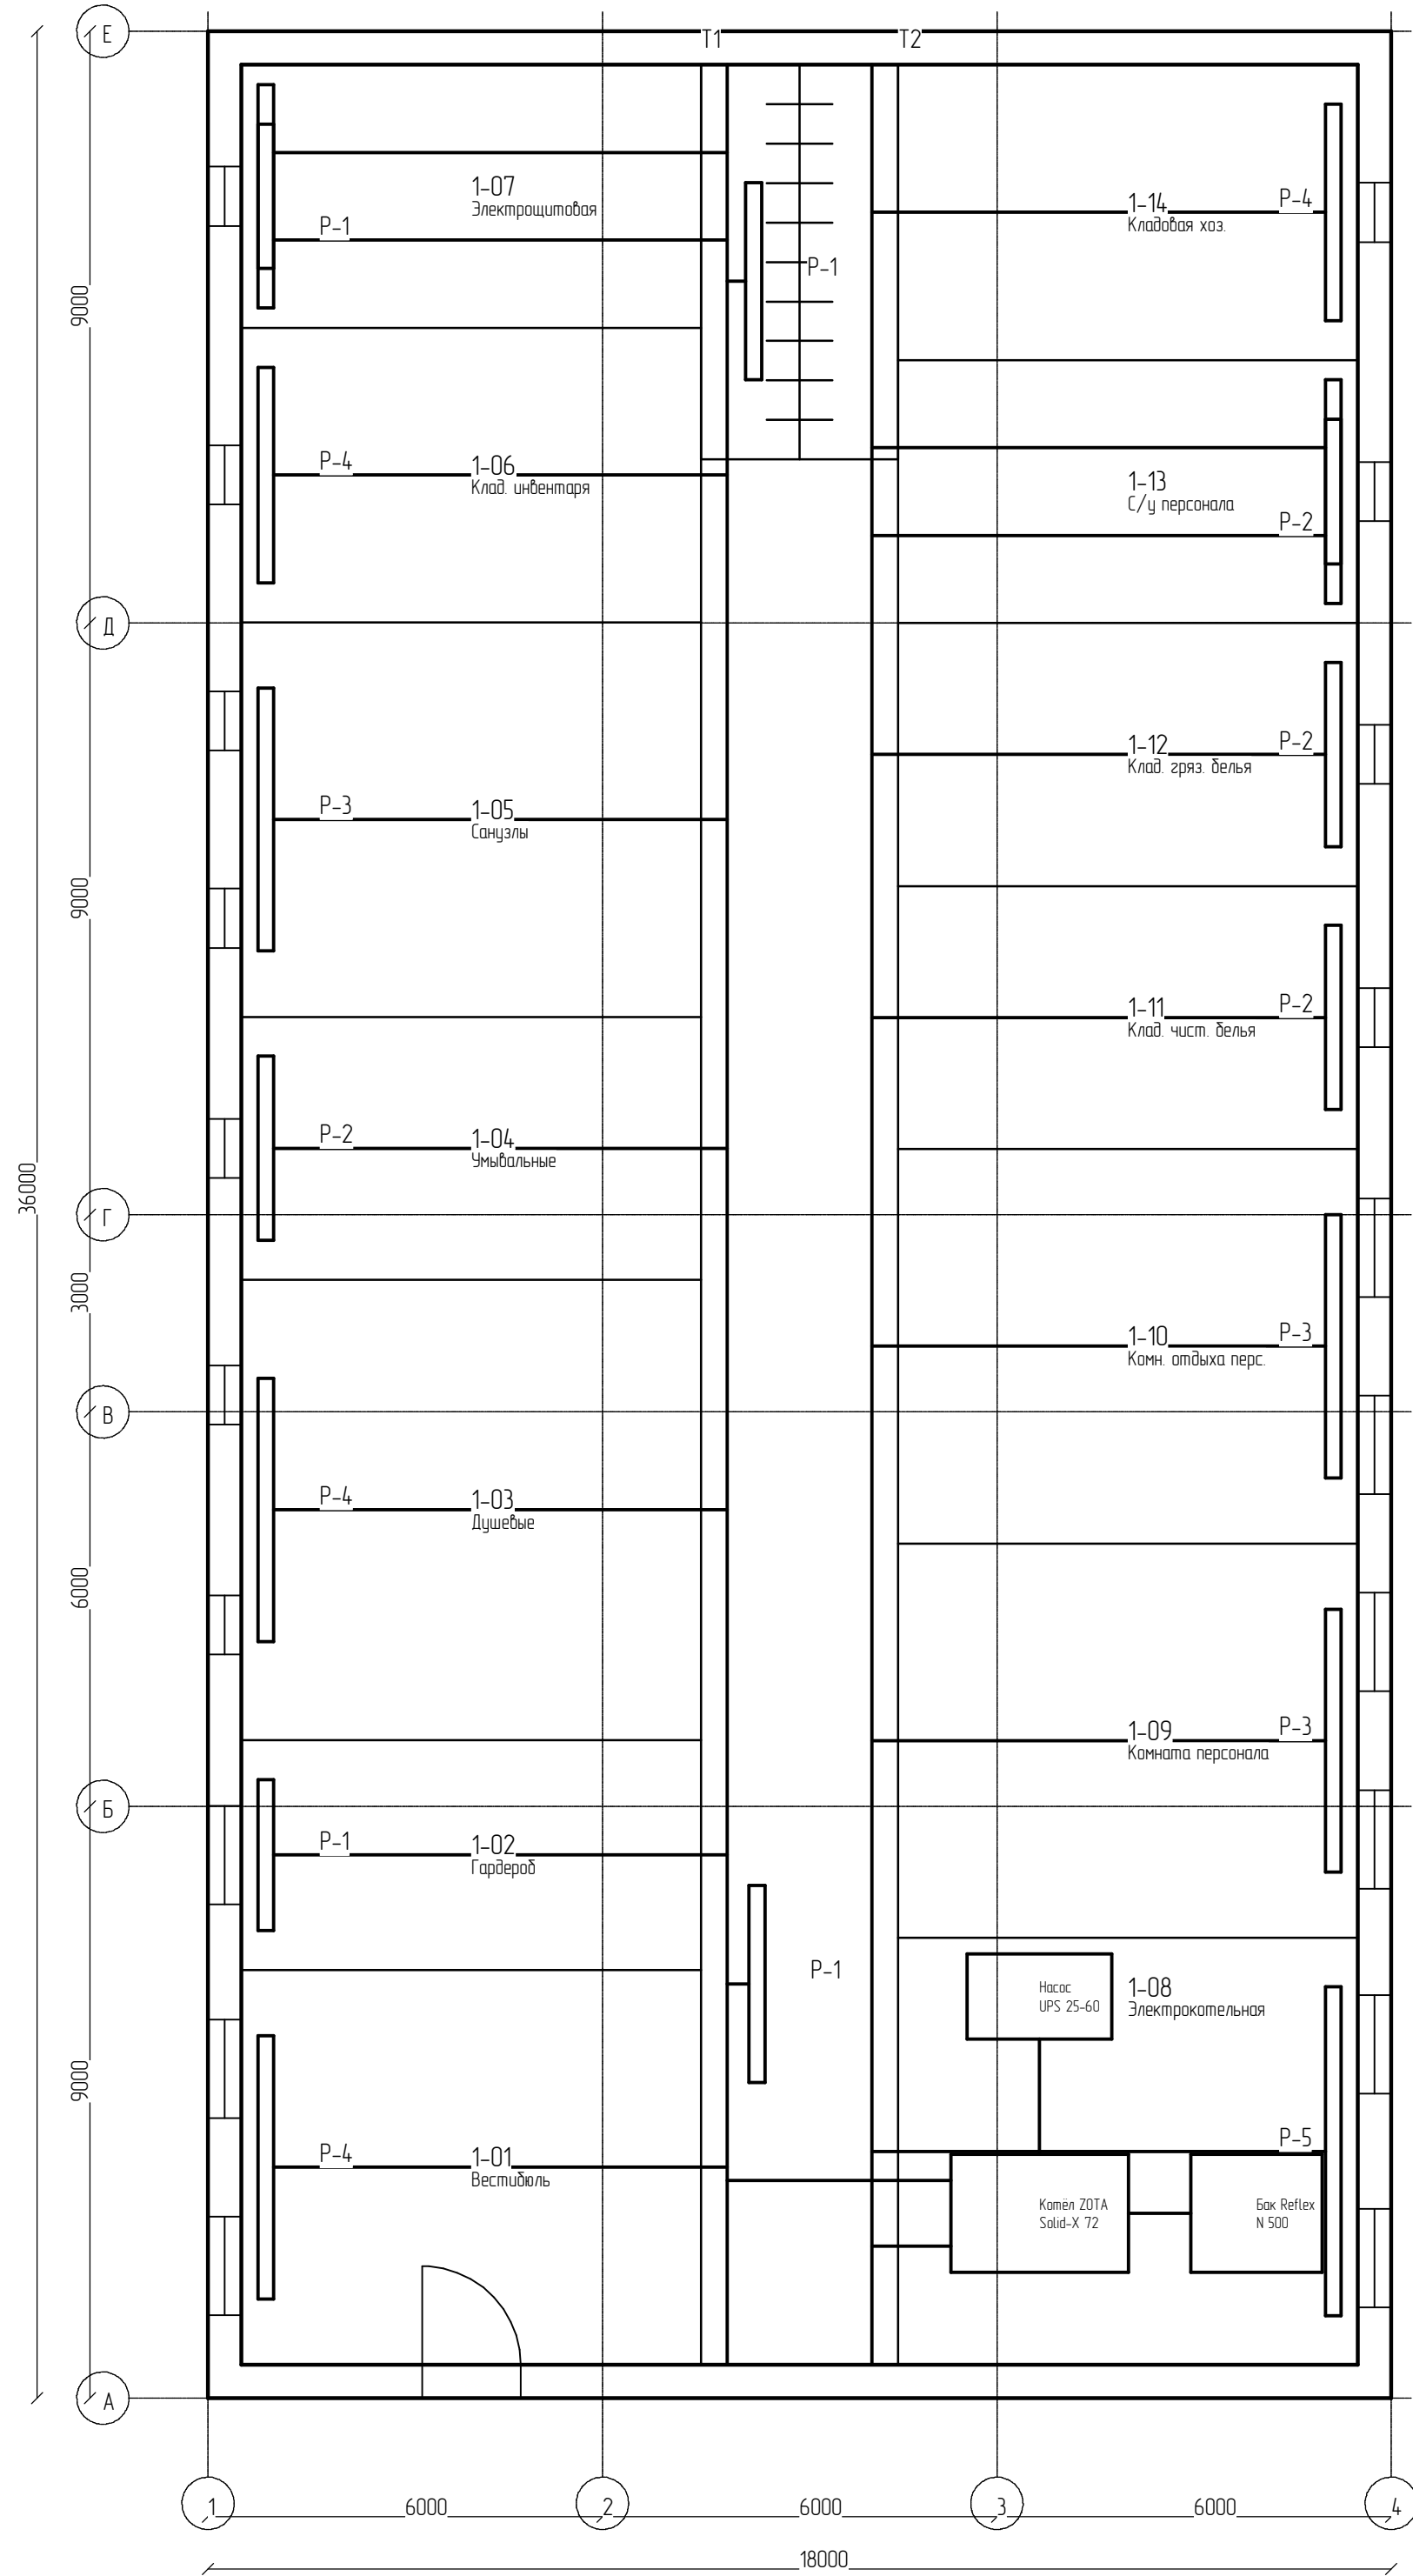

План 2-го этажа. Система отопления
М 1:100

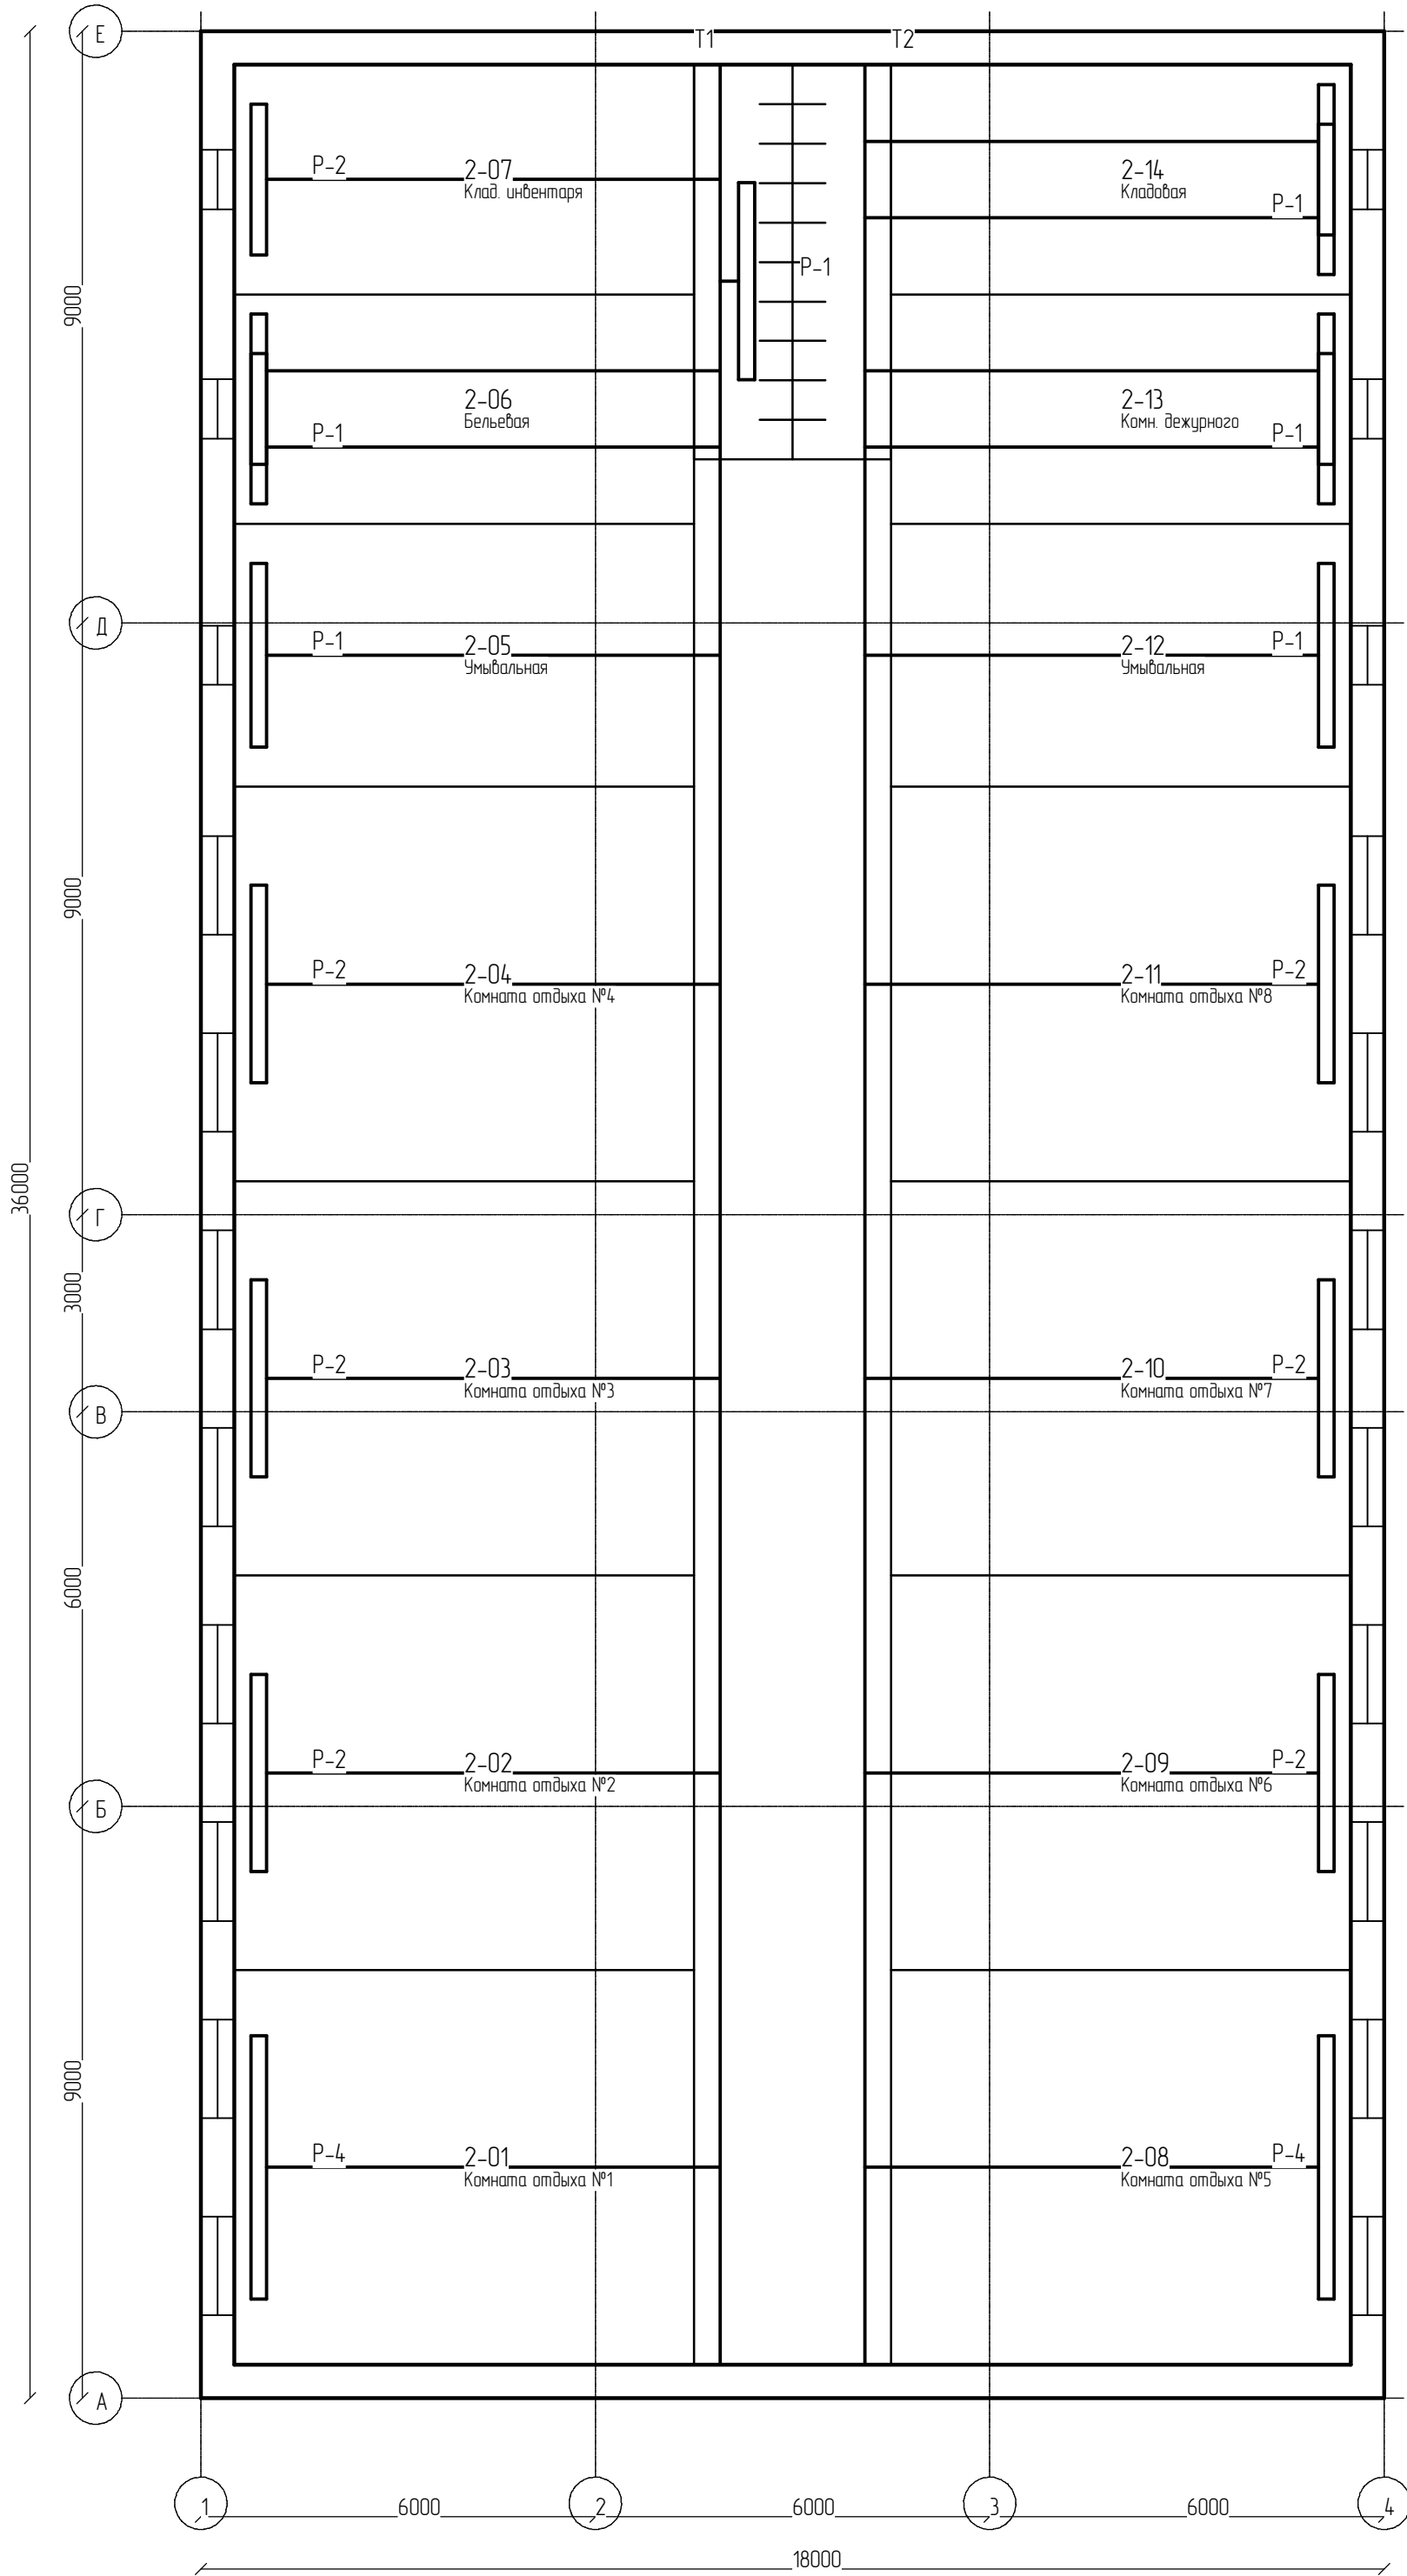

Экспликация помещений (1 этаж)			
№	Наименование	об, м	С, м²
1-01	Вестибиль	64,99	419
1-02	Гардероб	354,99	24,5
1-03	Душевые	74,99	48,9
1-04	Учбыльные	44,99	28
1-05	Санузлы	64,99	419
1-06	Клад инвентаря	4484,99	313
1-07	Электрощитовая	44,99	28
1-08	Электростанция	6494,99	454
1-09	Кантата персонала	64,99	419
1-10	Кант. отдыха перс.	64,99	419
1-11	Клад чист белья	44,99	28
1-12	Клад гряз белья	44,99	28
1-13	С/у персонала	44,99	28
1-14	Кладовая изз	4494,99	314
1-15	Коридор, лестничная клетка	36,9843	104,9

Условные обозначения	
	Регистр из стальных труб Ø108x4, Р-1, Р-5
	T1 – магистраль подающая
	T2 – магистраль обратная
	Стык, подбодка к прибору
	Электростанция ZOTA Solid-X 72
	Насос Grundfos UPS 25-60
	Бак расширительный Reflex N 500

- Примечания
- Система отопления двухтрубная с верхней разводкой
 - Теплоноситель – вода 95–70 °С; t_{ср} = 82,5 °С
 - Отопительные приборы – регистры из стальных труб Ø108x4 (ГОСТ 10704); окраска масляной краской в 2 слоя
 - Источник теплоты – электростанция ZOTA Solid-X 72 (72 кВт), помещенные электростанцией 1-08
 - Размеры на чертеже – в мм, отметки – в м.

Экспликация помещений (2 этаж)			
№	Наименование	об, м	С, м²
2-01	Кантата отдыха №1	64,99	419
2-02	Кантата отдыха №2	64,99	419
2-03	Кантата отдыха №3	64,99	419
2-04	Кантата отдыха №4	64,99	419
2-05	Учбыльная	44,99	28
2-06	Бельевая	3494,99	24,4
2-07	Клад инвентаря	3494,99	24,4
2-08	Кантата отдыха №5	64,99	419
2-09	Кантата отдыха №6	64,99	419
2-10	Кантата отдыха №7	64,99	419
2-11	Кантата отдыха №8	64,99	419
2-12	Учбыльная	44,99	28
2-13	Кант. дежурного	3494,99	24,4
2-14	Кладовая	3494,99	24,4
2-15	Коридор, лестничная клетка	36,9843	104,9

					МВБЧ.080301.018-0В			
					Бытовой корпус: дачы отдыха "Лубрава" Система отопления Планы 1 и 2 этажей	Лит	Масса	Масштаб
Изм./Лист	№ докум.	Подп.	Дата			4		1:100
Разраб.	Луканин А.В.							
Проб.	Полулях Г.И.							
Т.контр.						Лист	Листов	1
И.контр.	Перещин Р.В.					М.И. ВлГЧ		
Утв.	Шаргород Р.В.					СТ-122		