


АксонOMETрическая схема системы отопления

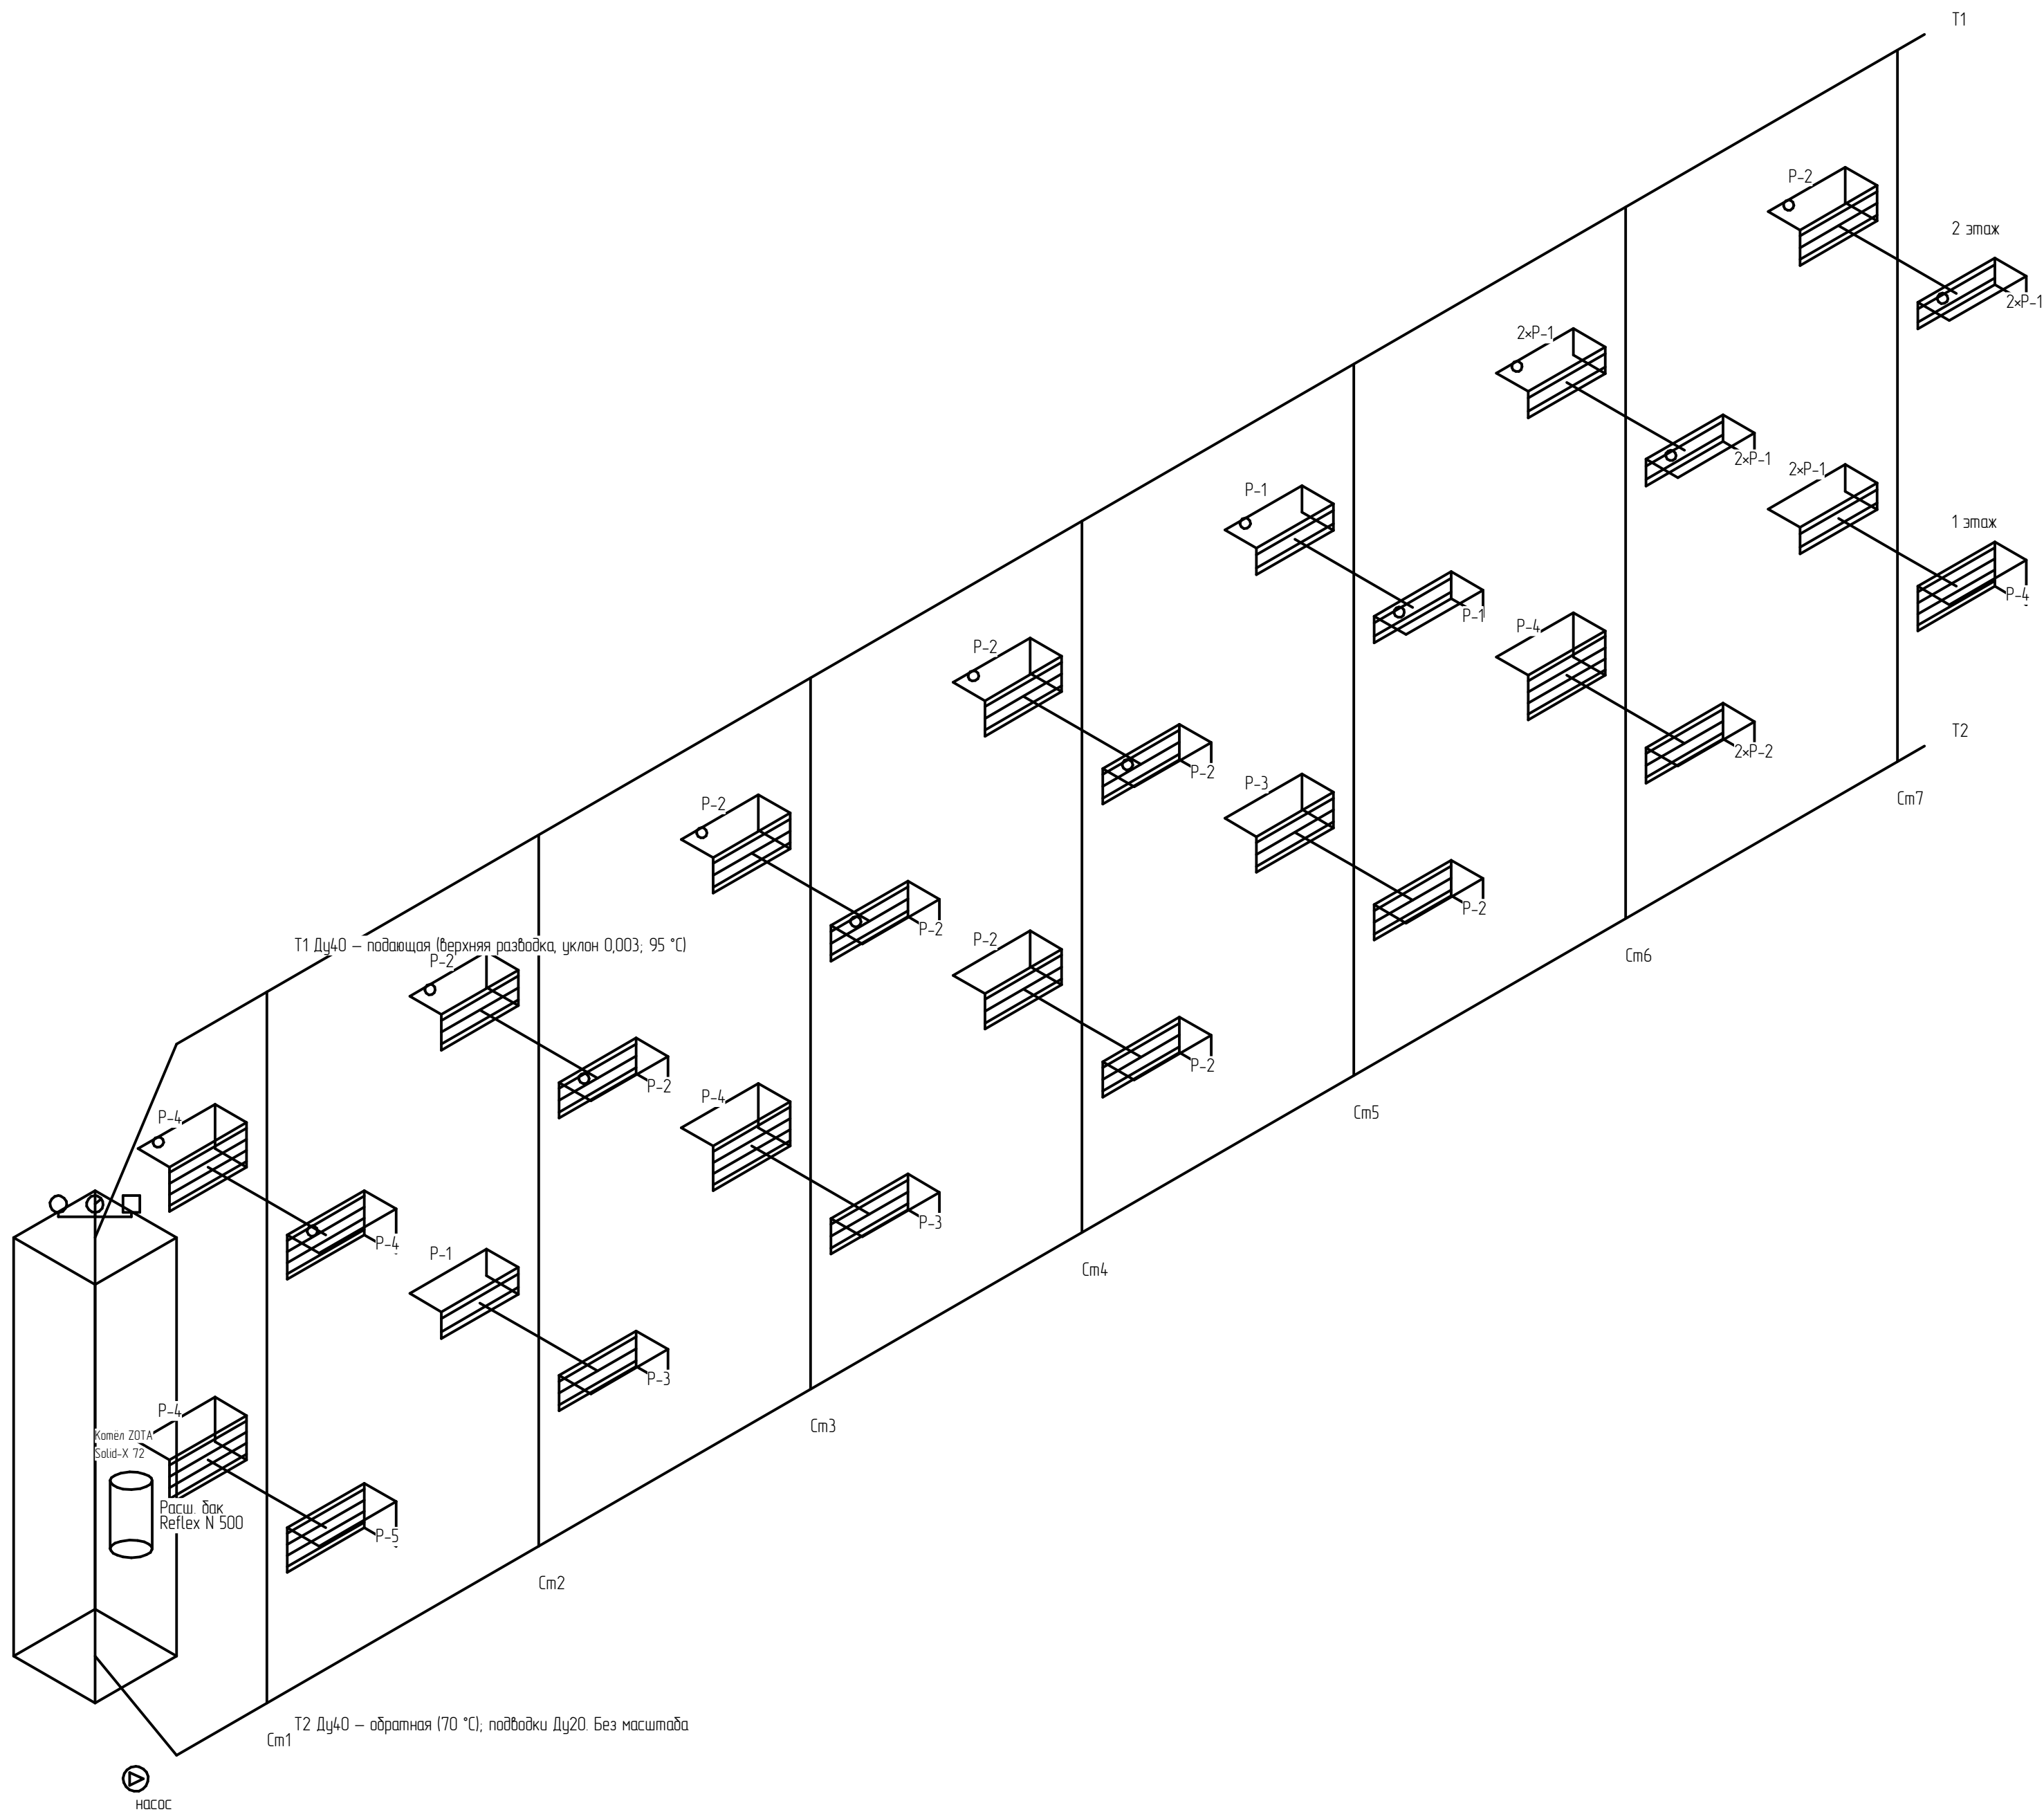

Ведомость отопительных приборов (регистры Ø108×4, ГОСТ 10704)

Марка	Труб п-Л, м	Q, Вт	Кол.	L труб, м
P-1 2×3,0		1366	14	84,0
P-2 3×3,0		1948	12	108,0
P-3 3×4,0		2598	3	36,0
P-4 4×4,0		3296	6	96,0
P-5 4×5,0		4120	1	20,0
Итого регистров Ø108×4			36	344,0

Примечания

- Система двухтрубная тупиковая с верхней разводкой; теплоноситель – вода 95–70 °С, t_{ср} = 82,5 °С.
- Приборы – регистры из гладких труб Ø108×4 (ГОСТ 10704), марки Р-1,Р-5, всего 36 шт, 344 п.м.
- Магистроли Т1/Т2 Ду40, подводы к приборам Ду20, стояки – по оси коридора, выпуски – к приборам этажей.
- Схема выполнена без масштаба, размеры – в мм.

				МВЧ.080301.018-0В						
Изм.	Лист	№ док.	Подп.	Дата	Бытовой корпус базы отдыха "Дубрава" Система отопления Аксонметрическая схема	Лист	Масса	Масштаб		
Разраб.		Лукашин А.О.				5		1:100		
Проб.		Полулях Г.И.				Лист 1				
Т.контр.						ММ ВЛГЧ СТ-122				
Н.контр.		Пердущин Р.В.								
Утв.		Шаропов Р.В.								
					Копировал					
					Формат А1					