


Схема подключения холодного водоснабжения (узел ввода и подпитки системы отопления). Без масштаба

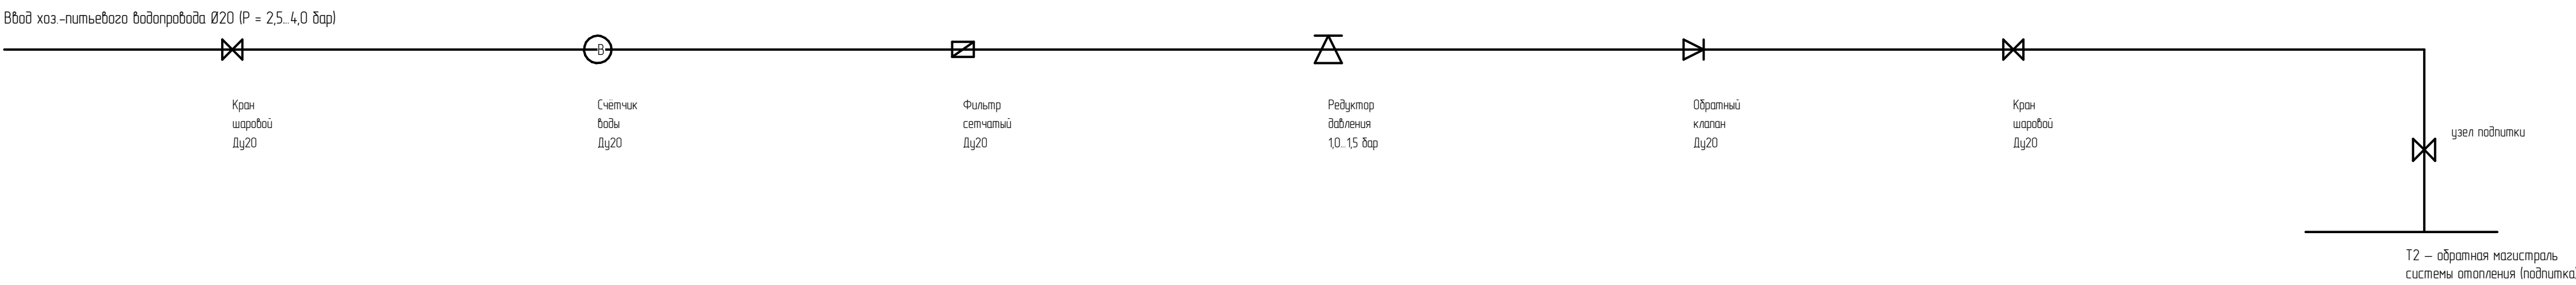

Спецификация узла ХВС / подпитки

Поз.	Наименование	Параметр / кол
1	Кран шаровый Ду20	2 шт
2	Счетчик воды крыльчатый	Ду20, 1 шт
3	Фильтр сетчатый кошач	Ду20, 1 шт
4	Редуктор давления	Ду20, 10...15 бар
5	Клапан обратный пружинный	Ду20, 1 шт
6	Трубопровод ХВС	сталь/ППР Ø20

Примечания

- подпитка системы отопления (V 2930 л) – из шах-путьевого
водопровода Ø20 через редуктор и обратный клапан
Редуктор настроен на давление выше статического давления
системы (P = 10 бар при остывании теплоносителя)
Обратный клапан исключает попадание теплоносителя в ХВС
Давление сети ХВС, счётчик и редуктор приняты по типовому
инженерному решению (в расчётной части не задавались)
Схема д/з настила, диаметры даны по ГОСТ

					МИВЧ.080301018-0В			
Изм	Лист	№ докм	Подп	Дата	Бытовой корпус базы отдыха "Дубрава" Водоснабжение холодное. Схема гидравлического подключения	Лит	Масса	Масштаб
Разраб	Лист	Акцион А.О.				6		1:100
Проб	Лист	Полулях Г.Л.						
Т.контр						Лист	Листов	1
И.контр	Перфилов Р.В.					МИ ВЛЧ СТ-122		
Утв	Шарандов Р.В.							